


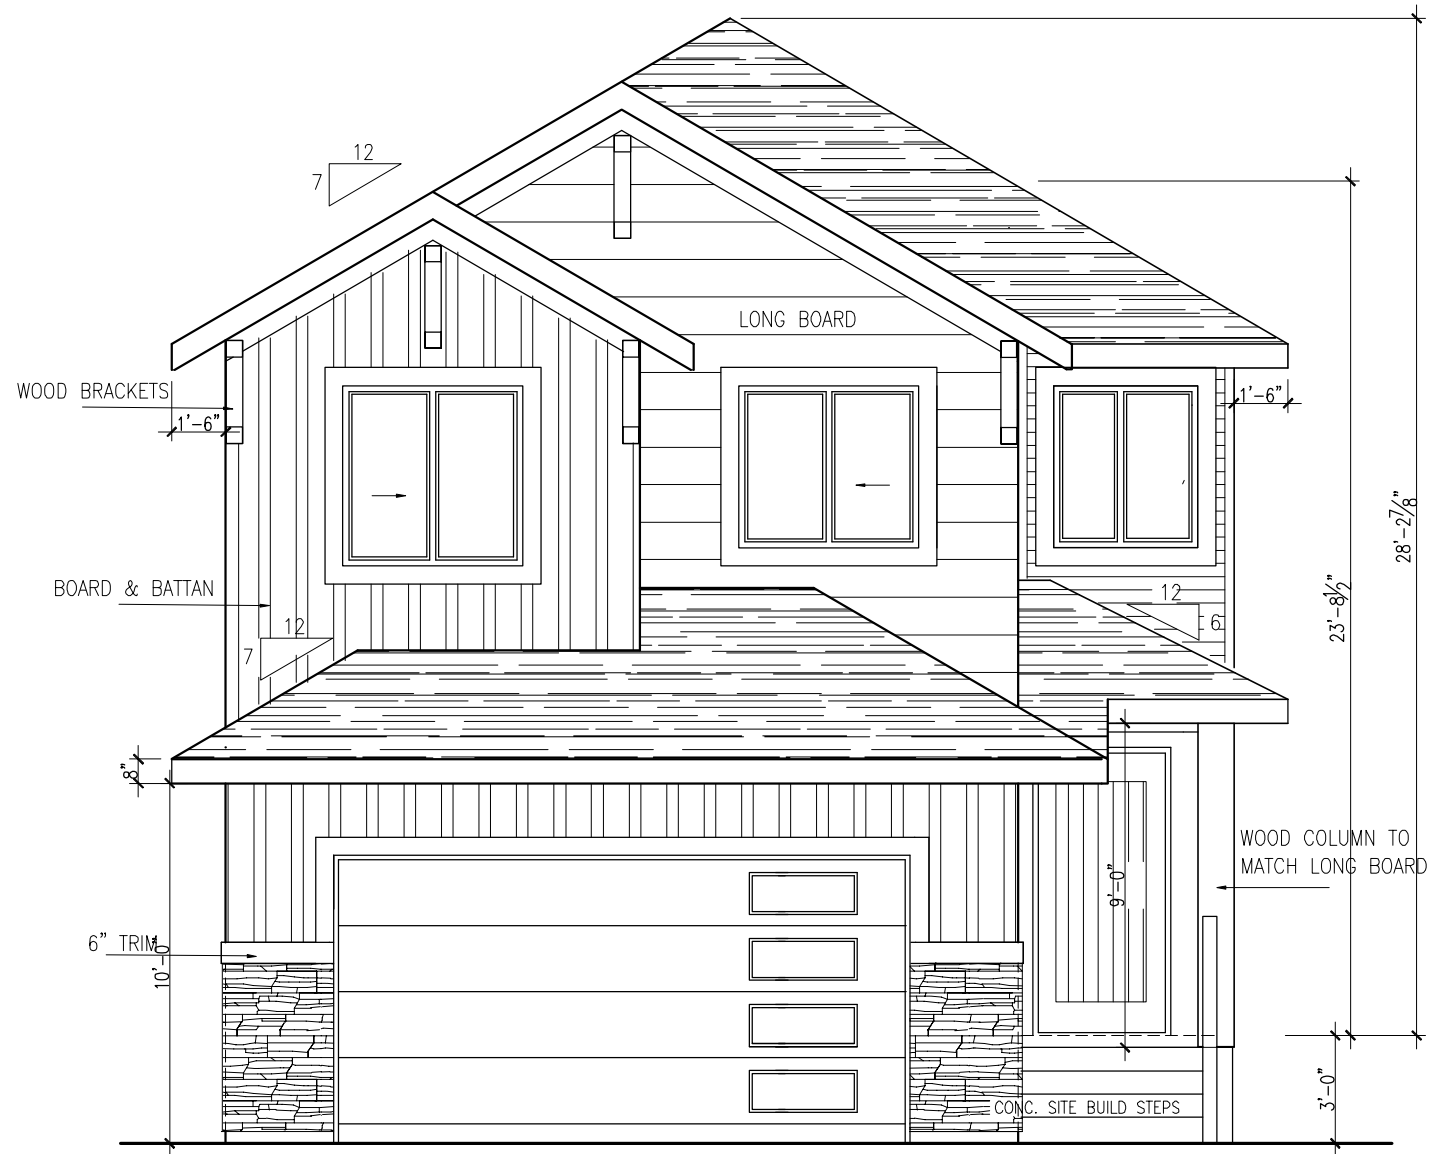

Front Elevation

SCALE 3/16"=1'-0"




Rear Elevation

SCALE 3/16"=1'-0"

Design Studio-1
for unique designs
 16508 - 20 Ave. SW, AB. T6W 5K1
 Ph: (780) 951 3628
 designstudio-1@hotmail.com

Sant Realty Ab.

AREA:	Scale: As Shown
Main Floor = 1,188 Sqft	Design by: Shahbaz
Upper Floor = 1,416 Sqft	Date: 17 Dec 2025
Total Area = 2,604 Sqft	
Lot : 55	Drawing
Blk.: 4	1 of 11
Plan : 252-0849	
18723 - 131 St NW	
Goodridge Corners	
Edmonton	

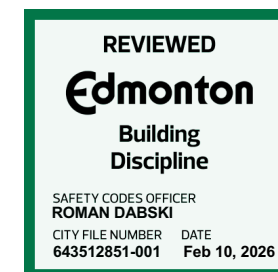

SPATIAL SEPARATION
REVIEWED



Left Elevation
SCALE 3/16"=1'-0"

Design Studio-1
for unique designs
16508 - 20 Ave. SW, AB. T6W 5K1
Ph: (780) 951 3628
designstudio-1@hotmail.com

Sant Reality Ab.	
AREA:	Scale: As Shown
Main Floor = 1,188 Sqft	Design by: Shahbaz
Upper Floor = 1,416 Sqft	Date: 17 Dec 2025
Total Area = 2,604 Sqft	
Lot : 55	Drawing 2 of 11
Blk.: 4	
Plan : 252-0849	
18723 - 131 St NW	
Goodridge Corners Edmonton	

REVIEWED
Edmonton
Building
Discipline
SAFETY CODES OFFICER
ROMAN DABSKI
CITY FILE NUMBER 643512851-001 DATE Feb 10, 2026

APPROVED
Edmonton
Development Permit
DEVELOPMENT AUTHORITY
EATHAN ROTH
CITY FILE NUMBER 643512851-002 DATE Feb 03, 2026

SPATIAL SEPARATION
REVIEWED



Right Elevation

SCALE 3/16"=1'-0"


Sant Reality Ab.

Design Studio-1
— for unique designs —
16508 - 20 Ave. SW, AB. T6W 5K1
Ph: (780) 951 3628
designstudio-1@hotmail.com

AREA:	Scale: As Shown
Main Floor = 1,188 Sqft	Design by: Shahbaz
Upper Floor = 1,416 Sqft	Date: 17 Dec 2025
Total Area = 2,604 Sqft	
Lot : 55	Drawing
Blk.: 4	3 of 11
Plan : 252-0849	
18723 - 131 St NW	
Goodridge Corners	
Edmonton	



Refer to pad footing charts for sizing information and applicable reinforcing details.

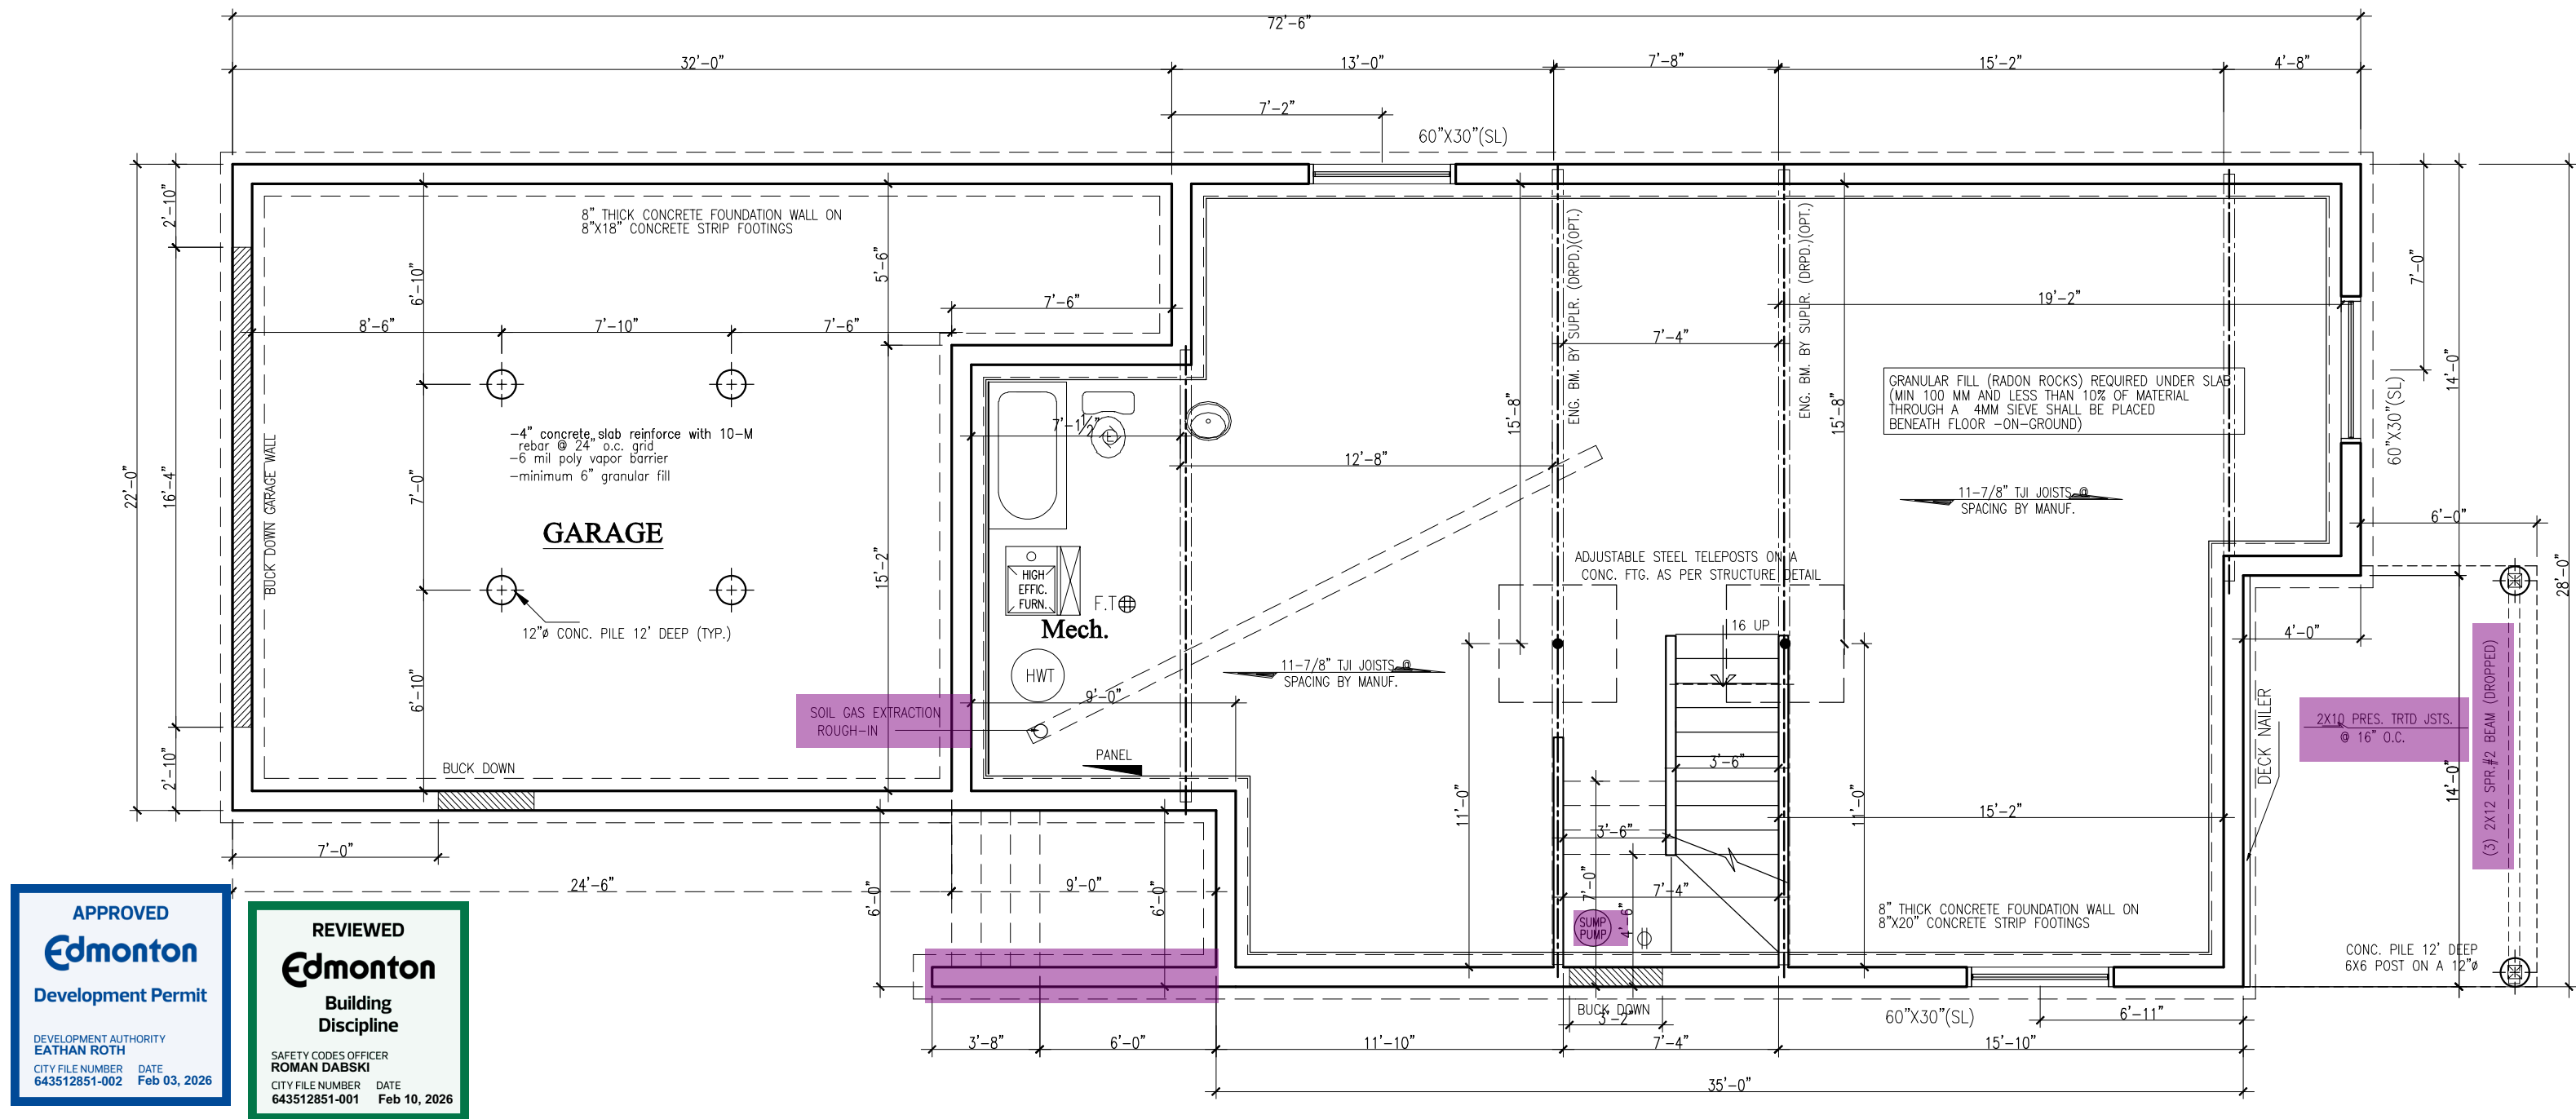

Sant Reality Ab.

Design Studio-1
for unique designs
16508 - 20 Ave. SW, AB. T6W 5K1
Ph: (780) 951 3628
designstudio-1@hotmail.com

AREA:	Scale: As Shown
Main Floor = 1,188 Sqft	Design by: Shahbaz
Upper Floor = 1,416 Sqft	Date: 17 Dec 2025
Total Area = 2,604 Sqft	
Lot : 55	Drawing
Blk.: 4	4 of 11
Plan : 252-0849	
18723 - 131 St NW	
Goodridge Corners	
Edmonton	

Foundation Plan


SCALE : 3/16"=1'-0"

EGRESS WINDOW **MINIMUM** REQUIREMENTS:
SEE NBC(AE): DIV B: 9.9.10.1
380 mm (15 inch) OF CLEAR HEIGHT AND WIDTH
0.35 sq m (3.77 sq ft) OF UNOBSTRUCTED OPEN AREA
760 mm (30 inch) WELL IN FRONT OF WINDOW WHERE REQUIRED

EGRESS WINDOW **MINIMUM** REQUIREMENTS:
SEE NBC(AE): DIV B: 9.9.10.1
380 mm (15 inch) OF CLEAR HEIGHT AND WIDTH
0.35 sq m (3.77 sq ft) OF UNOBSTRUCTED OPEN AREA
760 mm (30 inch) WELL IN FRONT OF WINDOW WHERE REQUIRED

AREA: Main Floor = 1,188 Sqft Upper Floor = 1,416 Sqft Total Area = 2,604 Sqft	Scale: As Shown Design by: Date: Shahbaz 17 Dec 2025
Lot : 55 Blk.: 4 Plan : 252-0849 18723 - 131 St NW Goodridge Corners Edmonton	Drawing 4a & 11

ATTIC ACCESS AS PER NBC 2023(AE) 9.19.2.1

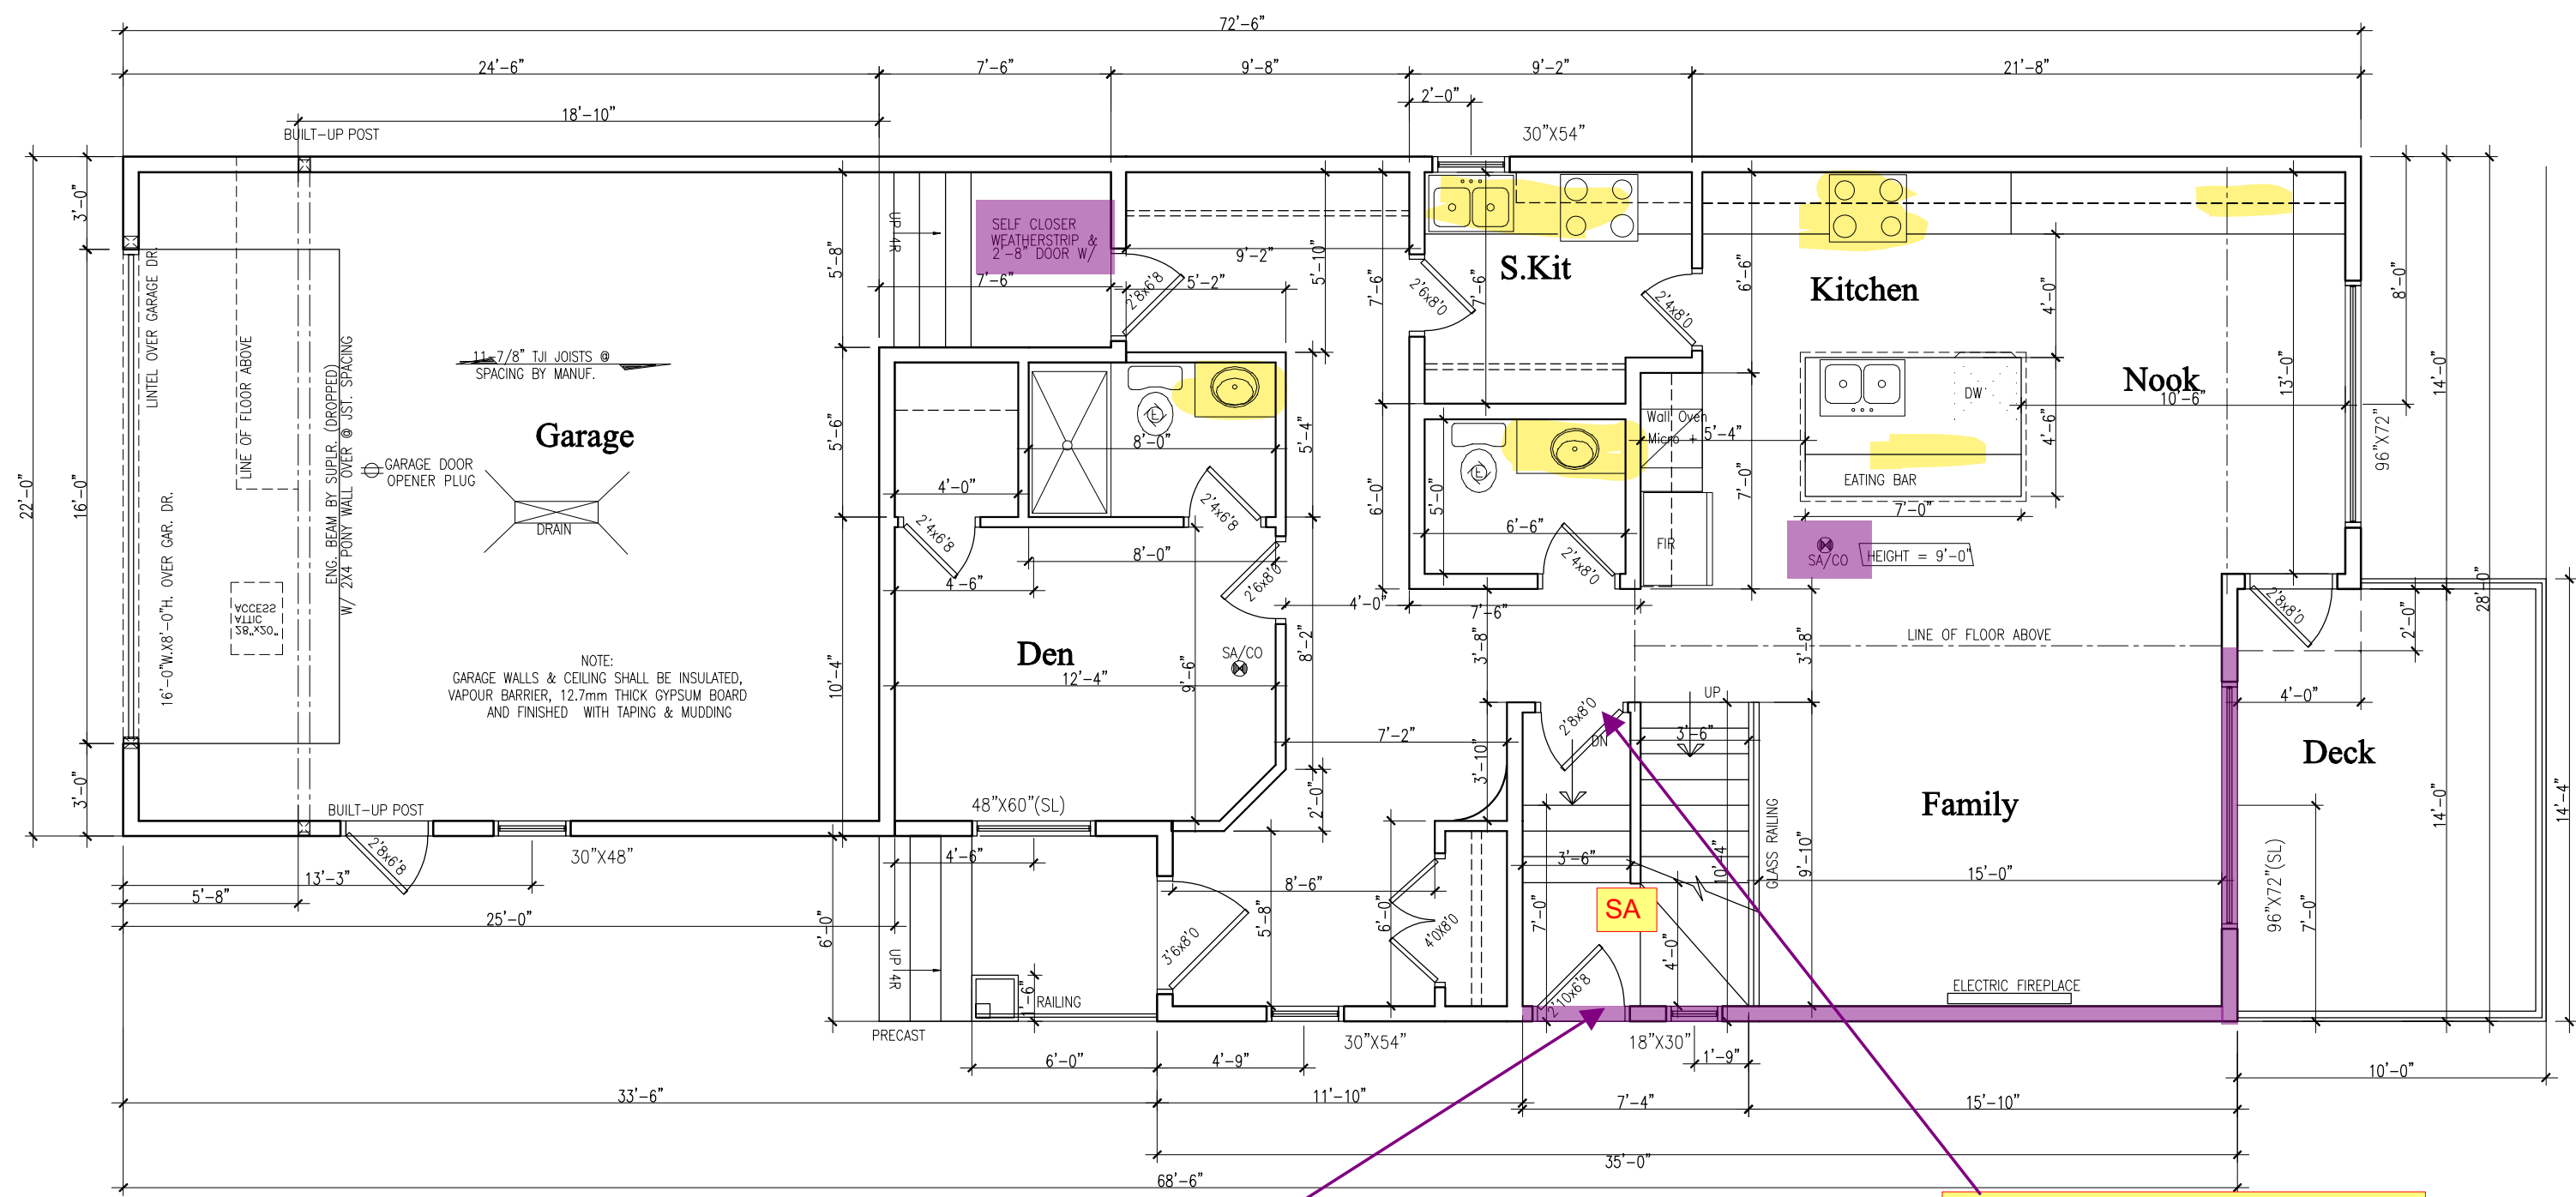

SUITE ENTRANCE

DOUBLE Lockable Door: 45mm solid core door (20 min FP) self closing

Main Floor Plan

1188 Sqft

SCALE : 3/16"=1'-0"

APPROVED

Edmonton

Development Permit

DEVELOPMENT AUTHORITY

EATHAN ROTH

CITY FILE NUMBER DATE

643512851-002 Feb 03, 2026

REVIEWED

Edmonton

Building Discipline

SAFETY CODES OFFICER

ROMAN DABSKI


CITY FILE NUMBER DATE

643512851-001 Feb 10, 2026

Design Studio-1
for unique designs
16508 - 20 Ave. SW, AB. T6W 5K1
Ph: (780) 951 3628
designstudio-1@hotmail.com

Sant Reality Ab.	
AREA:	Scale: As Shown
Main Floor = 1,188 Sqft	Design by: Shahbaz
Upper Floor = 1,416 Sqft	Date: 17 Dec 2025
Total Area = 2,604 Sqft	
Lot : 55	Drawing 5 of 11
Blk.: 4	
Plan : 252-0849	
18723 - 131 St NW	
Goodridge Corners	
Edmonton	

ALL Sleeping rooms to meet NBC2023 (AE): 9.9.10.1
ATTIC ACCESS AS PER NBC 2023(AE) 9.19.2.1

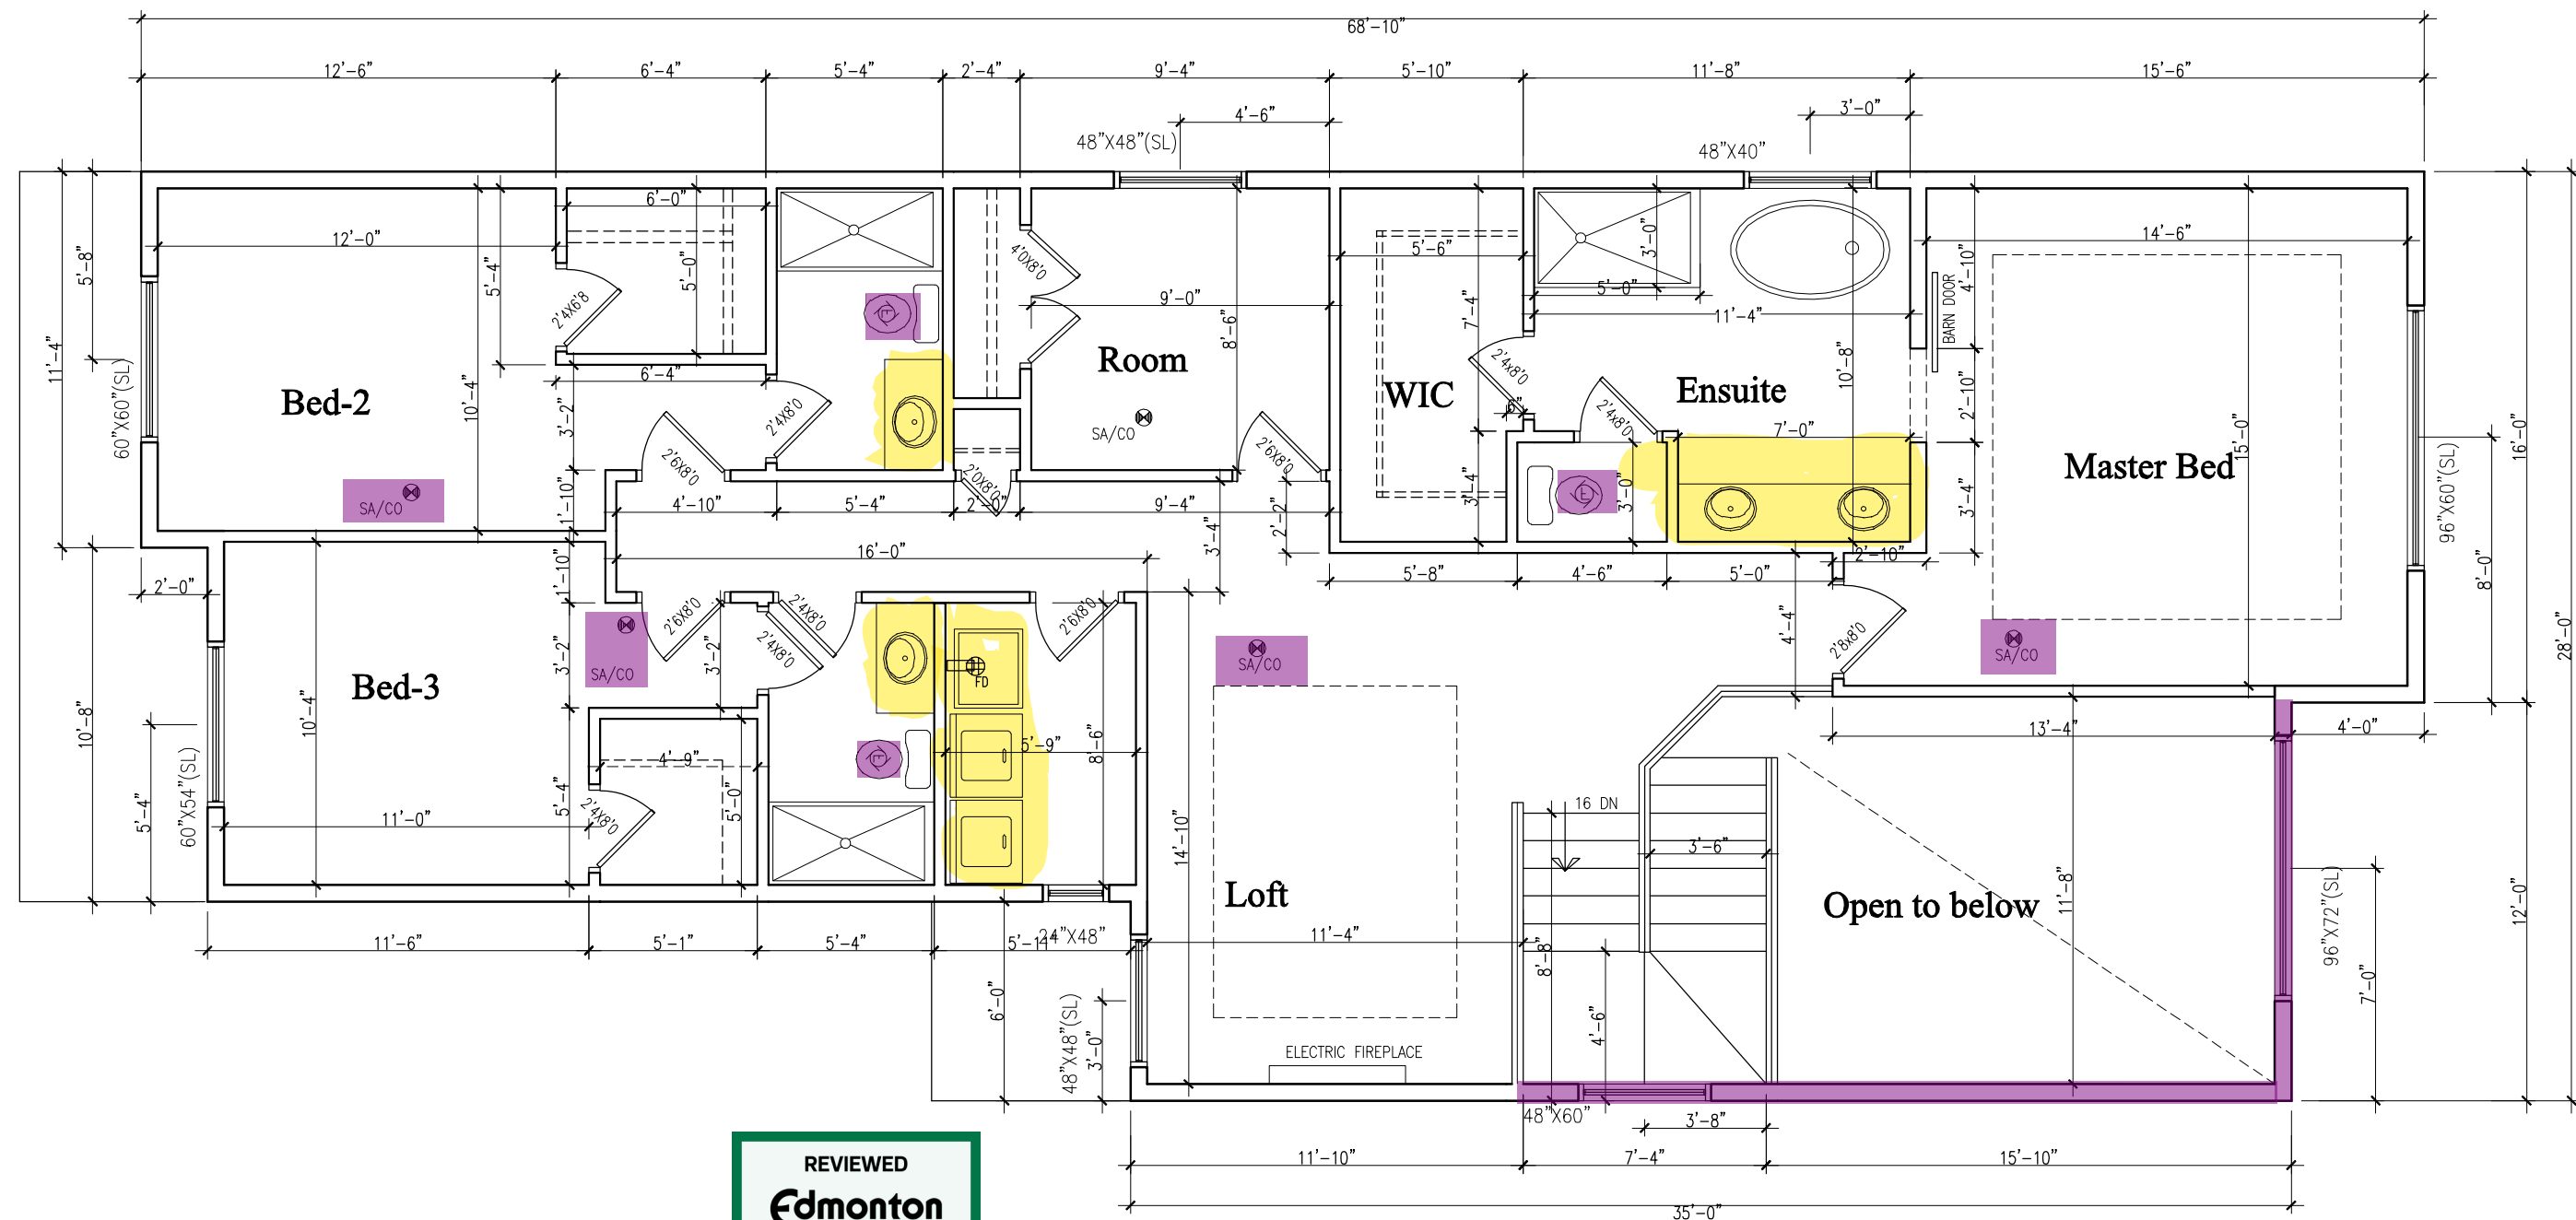

Upper Floor Plan


SCALE : 3/16"=1'-0"

1416 Sqft

Design Studio-1
for unique designs
16508 - 20 Ave. SW, AB. T6W 5K1
Ph: (780) 951 3628
designstudio-1@hotmail.com

Sant Reality Ab.

AREA:	Scale: As Shown
Main Floor = 1,188 Sqft	Design by: Shahbaz
Upper Floor = 1,416 Sqft	Date: 17 Dec 2025
Total Area = 2,604 Sqft	
Lot : 55	Drawing
Blk.: 4	6 of 11
Plan : 252-0849	
18723 - 131 St NW	
Goodridge Corners	
Edmonton	

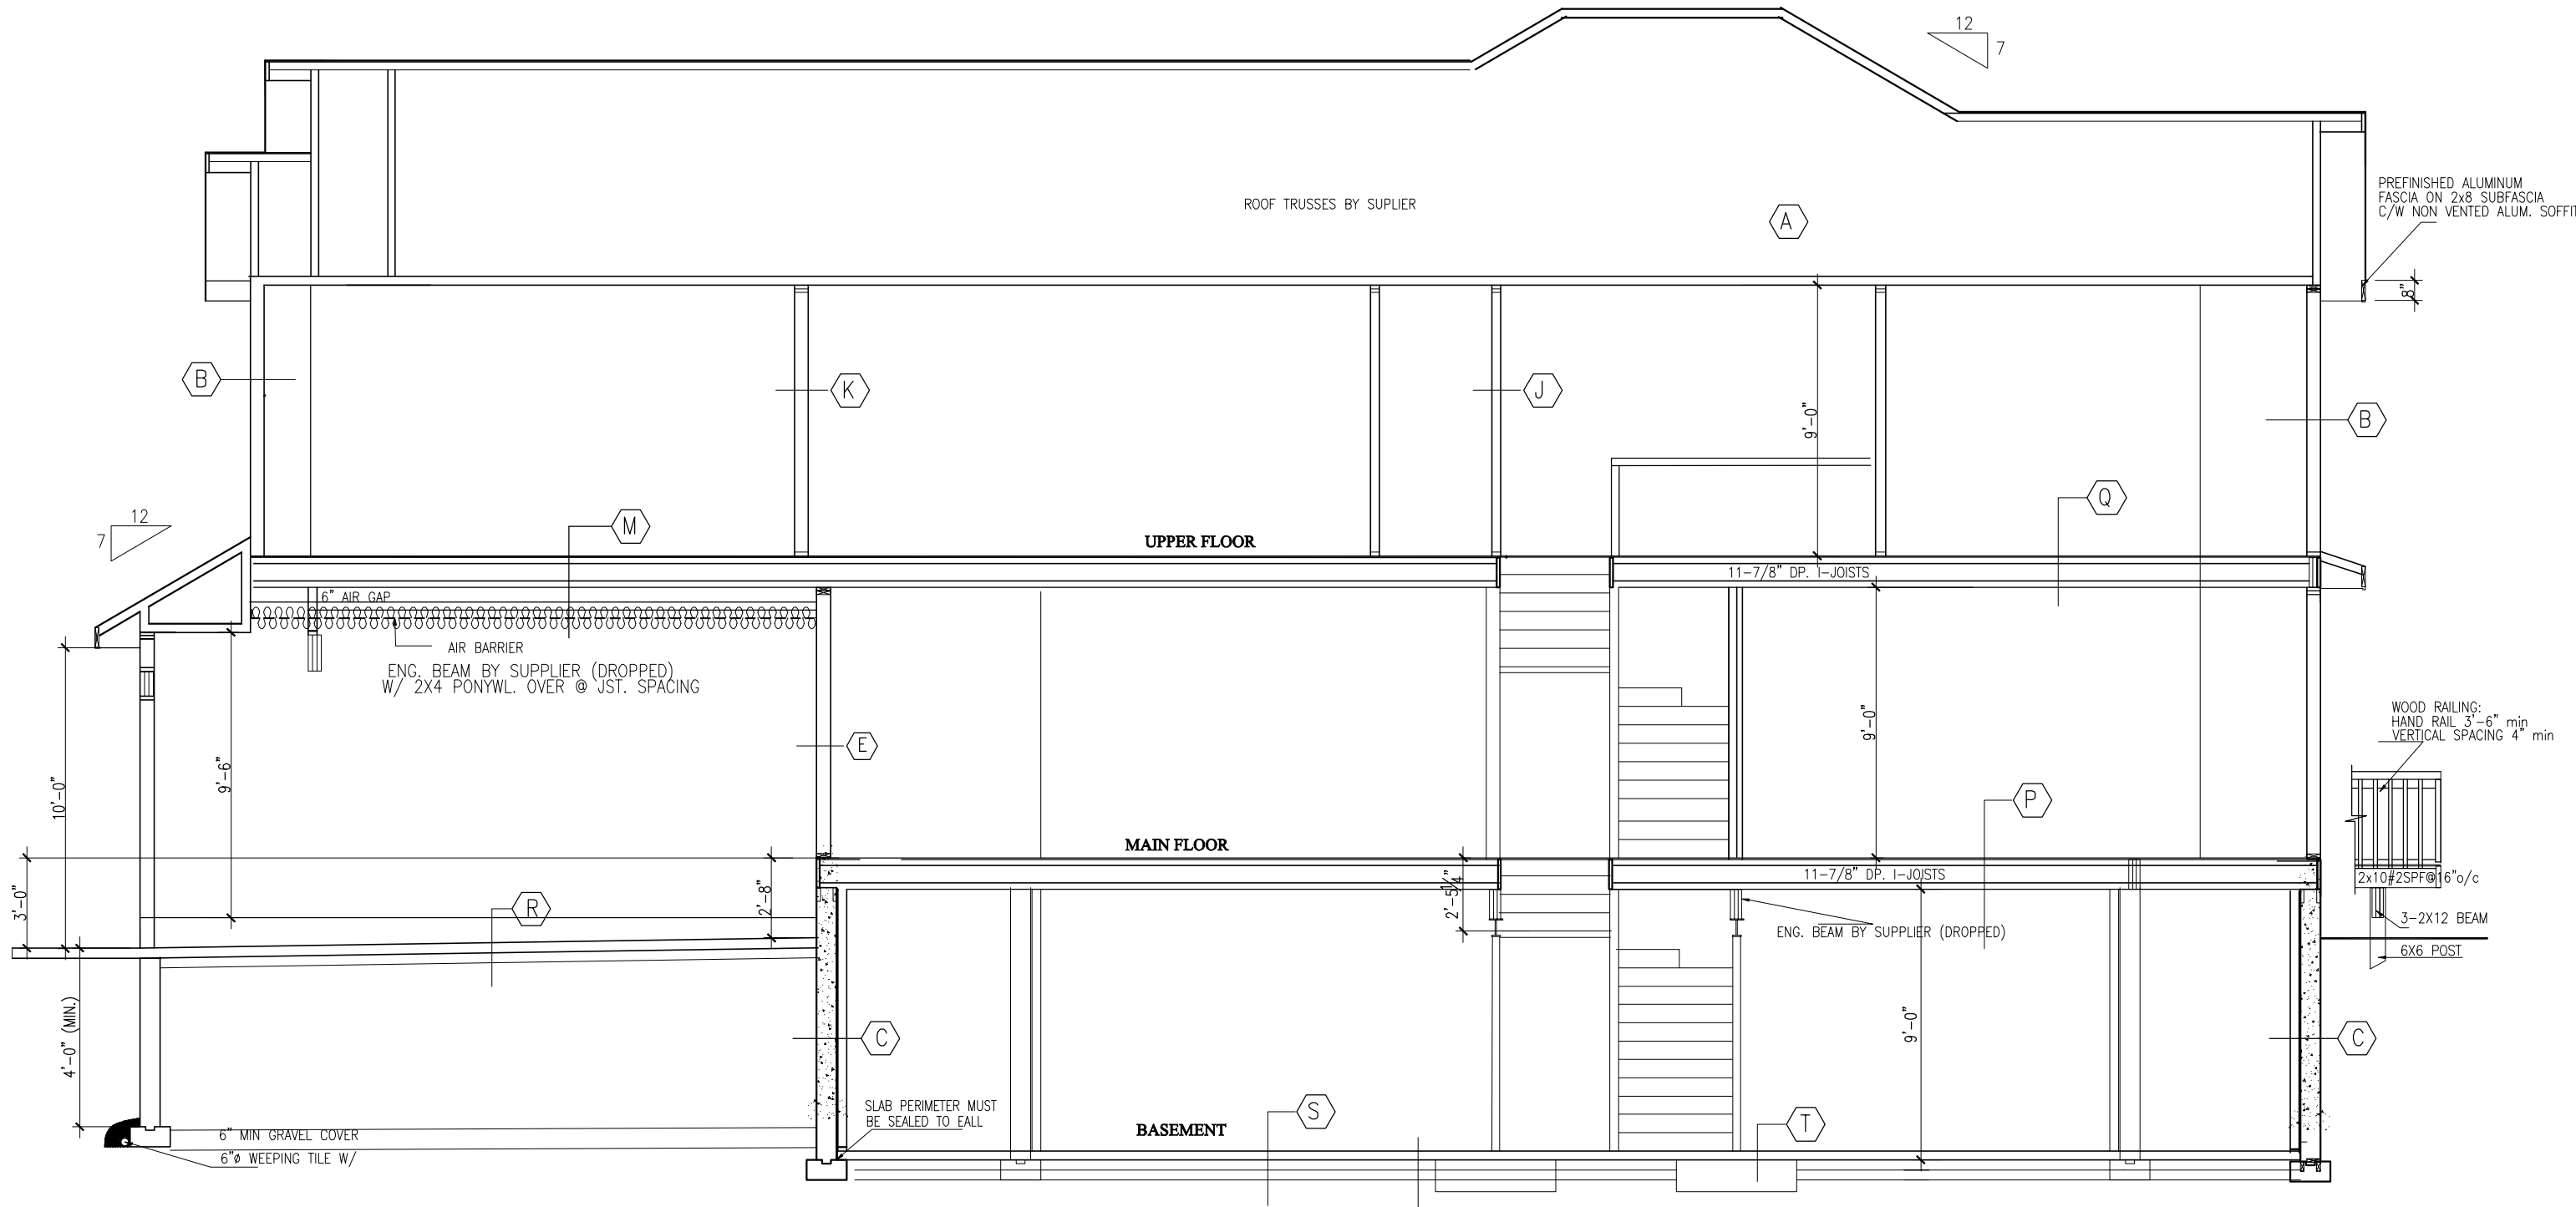

Cross Section (typ.)
SCALE 3/16"=1'-0"

NOTE:
GRADE SHOWN IS FOR DRAWING PURPOSES ONLY. ACTUAL GRADE SHALL BE DETERMINED ON SITE.

NOT LESS THAN 100mm OF COARSE CLEAN GRANULAR MEATERIAL (RADON ROCKS)
CONTAINING NOT MORE THAN 10% OF MATERIAL THAT WILL PASS
A 4MM SIEVE SHALL BE PLACED BENEATH FLOOR-ON-GROUND.
A ROUGH-IN-FOR RADON EXTRAC TION TO EITHER PERFORMANCE OR
PRESCRIPTIVE REQUIREMENTS MUST BE INSTALLED.(SEE DETAIL B)
POLYTHYLENE SOIL GAS BVARRIER IS REQUIRED UNDER SLAB

Design Studio-1
for unique designs

16508 - 20 Ave. SW,AB. T6W 5K1
Ph: (780) 951 3628
designstudio-1@hotmail.com

Sant Reality Ab.	
AREA:	Scale: As Shown
Main Floor = 1,188 Sqft	Design by: Shahbaz
Upper Floor = 1,416 Sqft	Date: 17 Dec 2025
Total Area = 2,604 Sqft	
Lot : 55	Drawing 7 of 11
Blk.: 4	
Plan : 252-0849	
18723 - 131 St NW	
Goodridge Corners	
Edmonton	

REVIEWED

Edmonton

Building
Discipline

SAFETY CODES OFFICER
ROMAN DABSKI
CITY FILE NUMBER DATE
643512851-001 Feb 10, 2026

APPROVED

Edmonton

Development Permit

DEVELOPMENT AUTHORITY
EATHAN ROTH
CITY FILE NUMBER DATE
643512851-002 Feb 03, 2026

P

MAIN FLOOR

FLOOR FINISH
(CARPET W/ UNDERLAY OR
LINO W/ K3 UNDER)
23/32 T&G SUBFLOOR
(GLUED,SCREWED & NAILED)
ENGINEERED I JOISTS AS PER STRUCTURE
BRIDGING @ 7' O.C IF REQUIRED

Q

UPPER FLOOR

FLOOR FINISH
(CARPET W/ UNDERLAY OR
LINO W/ K3 UNDER)
23/32 T&G SUBFLOOR
(GLUED,SCREWED & NAILED)
ENGINEERED I JOISTS AS PER STRUCTURE
1/2" GYPSUM BOARD WITH TEXTURE

R

CONC. FLOOR (GARAGE)

4" CONCRETE SLAB REINFORCE WITH 10-M
REBAR @ 18" o.c. GRID & DOWEL REBAR
INTO FOUNDATION WALL &/OR GARAGE WALL
8" MIN. GRANULAR FILL
4" min. SLOP TO FRONT

S

CONC. FLOOR (Basement)

4" CONCRETE SLAB REINFORCE WITH 10-M
REBAR @ 24" O.C EACH WAY
6 (mil) POLY VAPOUR BARRIER
6" MIN. GRANULAR FILL


T

POST FOOTING


3" DIA TELEPOST ON TOP OF
48"x48"x8"CONC. FTG.
R/w 4-10M BARS
EACH WAY@3"FROM BOTTOM

GENEAL CONSTRUCTION NOTES:

- 1. FINISHED WOOD RAILINGS – SPINDLW SPACING MAX. 4" APART.
- 2. FORNT ENTRY STEP TO BE PRECAST CONCRETE
- 3. PROVIDE ONE CAPPED DRYER VENT.
- 4. 20"x28"(MIN.) INSULATED ATTIC ACCESS HATCH W/INSULATION SHAFT
- 5. FURNACE CHIMNEY TO EXTEND 2'-0 ABOVE RIDGE OR HIGHEST POINT OF ROOF WITH IN THE HORIZONTAL DISTANCE OF 10'-0(WHICH EVER IS CLOSER)
- FIRE PLACE CHIMNEY'S TO BE EXTENDED MIN. 3'-0 (SIMILAR TO FURNANVE FLUE)
- 6. PROVIDE 4-14" DEEP SHELVES (MIN.)
- 7. PROVIDE FLASHING ABOVE ALL EXTERIOR DOOR & WINDOW OPENINGS

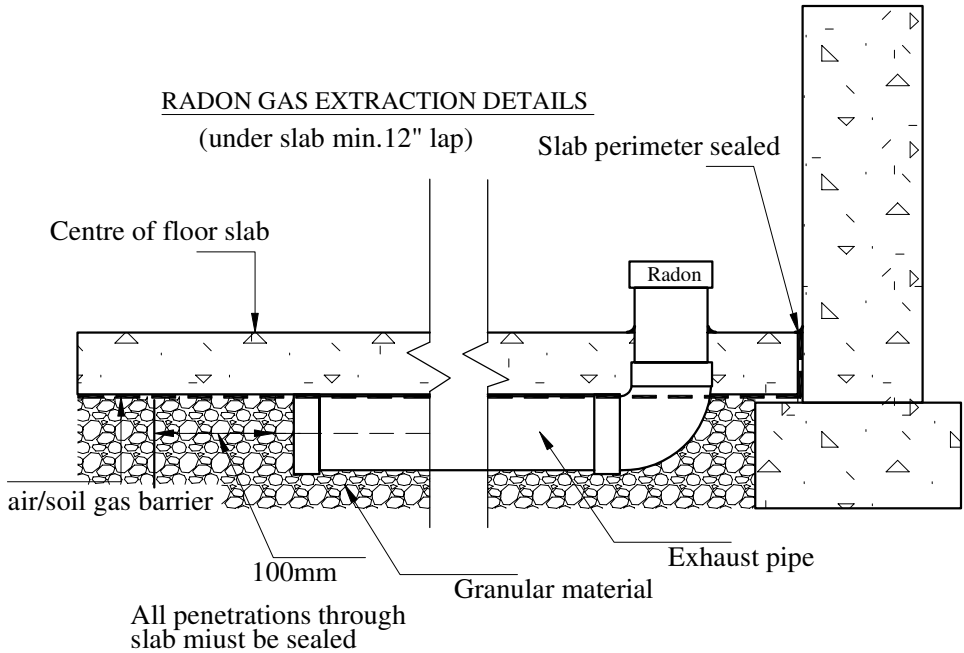

45 MINUTE FIRE RATED
(EXTERIOR WALL)

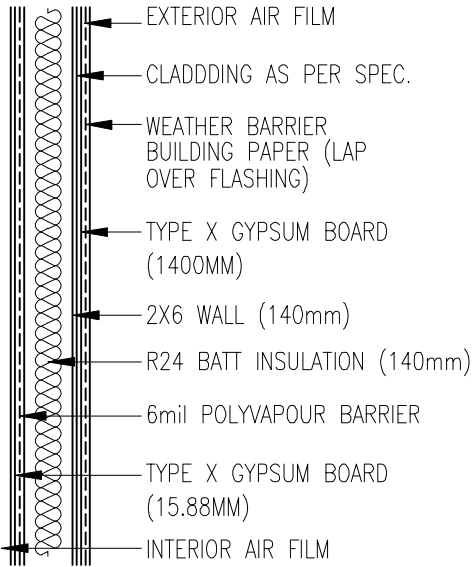

45 min EXTERIOR WALL HOUSE (RSI 2.97)

(TABLE: 9.36.2.6.B)	RSI
OUTSIDE AIR FILM	0.03
CLADDING MATERIAL (MINIMUM)	0.11
ASHPHALT IMPREGNATED PAPER	
TYPE X GYPSUM (15.88MM)	0.100
FIRE RETARDANT OSB AS PER VARIANCE	
2x6 STUD FRAMING @24"O.C.	2.66
R24 BATT INSULATION	
6MIL. AIR BARRIER	
TYPE X GYPSUM BOARD (15.88mm)	0.100
INTERIOR AIR FILM	0.12
EFFECTIVE VALUE	3.130

Design Studio-1
— for unique designs —




16508 - 20 Ave. SW,AB. T6W 5K1
Ph: (780) 951 3628
designstudio-1@hotmail.com

Sant Reality Ab.


AREA:	Scale: As Shown
Main Floor = 1,188 Sqft	Design by: Shahbaz
Upper Floor = 1,416 Sqft	Date: 17 Dec 2025
Total Area = 2,604 Sqft	
Lot : 55	Drawing
Blk.: 4	9 of 11
Plan : 252-0849	
18723 - 131 St NW	
Goodridge Corners	
Edmonton	

REVIEWED
Edmonton
Building
Discipline

SAFETY CODES OFFICER
ROMAN DABSKI
CITY FILE NUMBER DATE
643512851-001 Feb 10, 2026

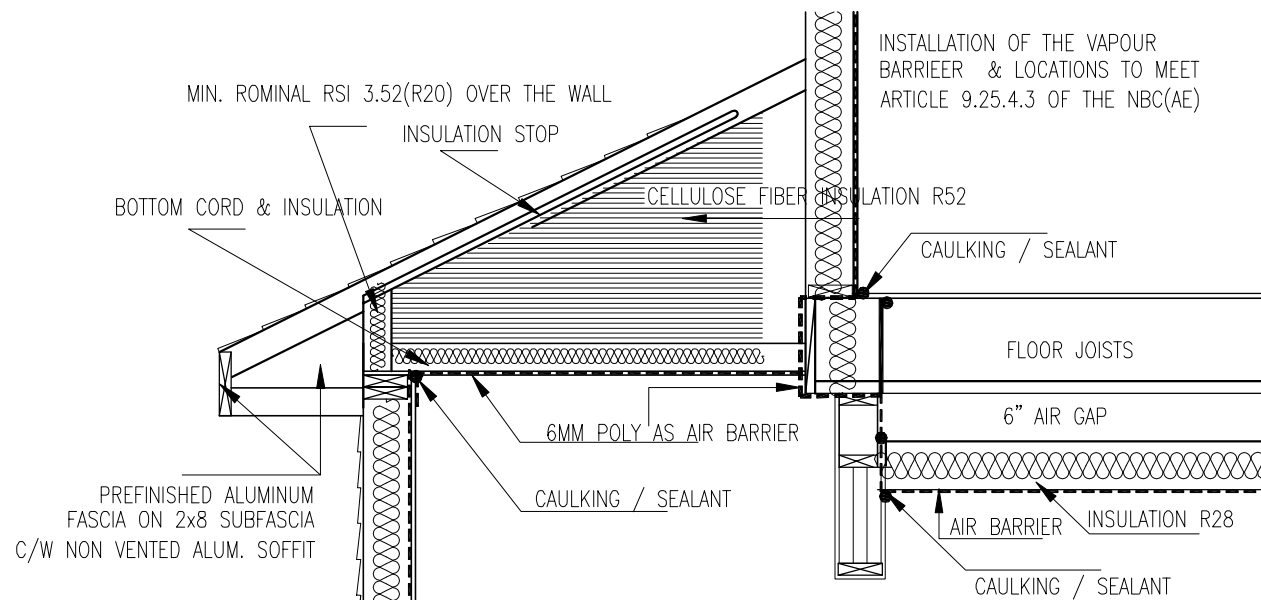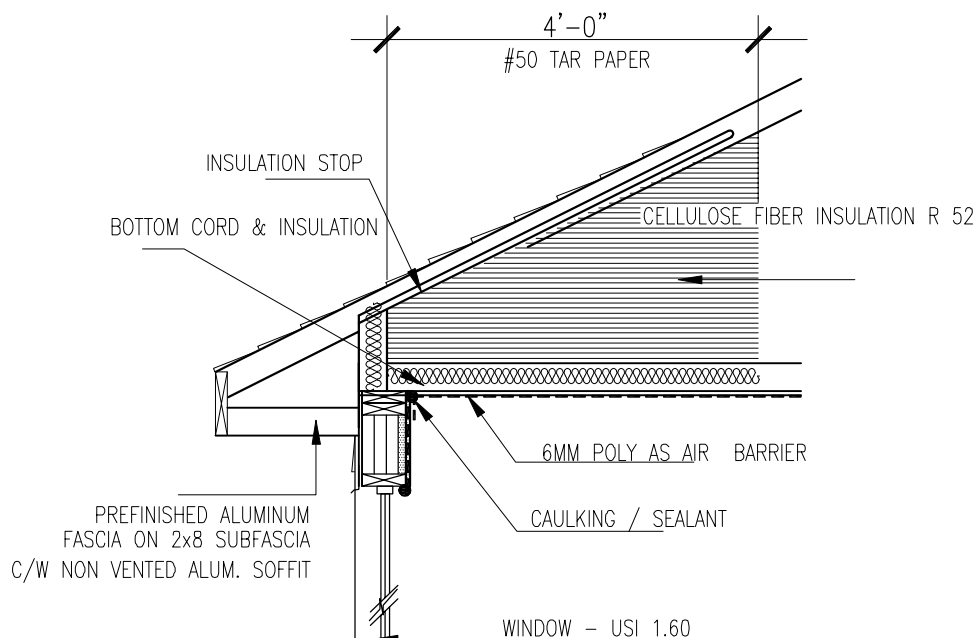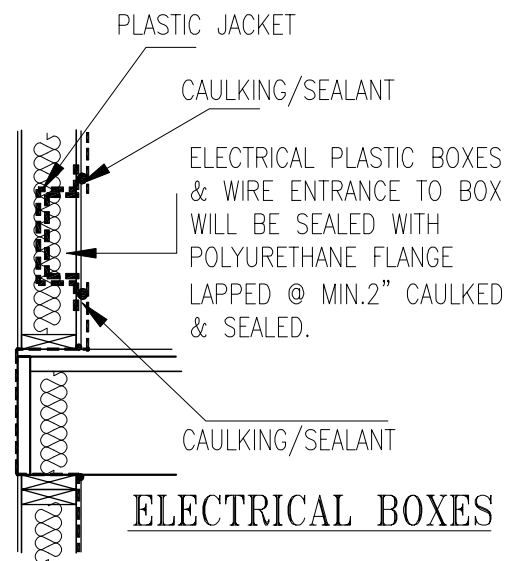


FLOOR OVER GARAGE

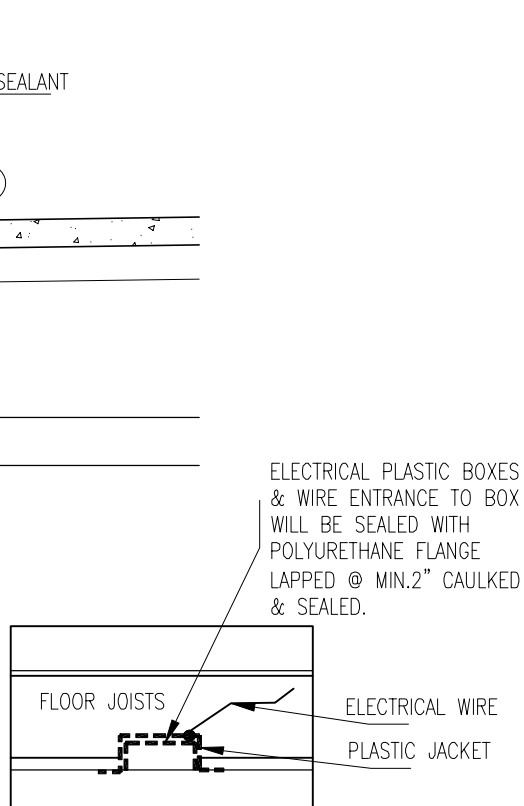

ELECTRICAL BOXES IN CEILING

ALL AIR BARRIER LAPS SHALL BE STRUCTURALLY SUPPORTED
INSTALL BOXES WITH FLANGE OR FRAME BLOCKS TO BE
STRUCTURALLY SUPPORTED ON ALL FOUR SIDES

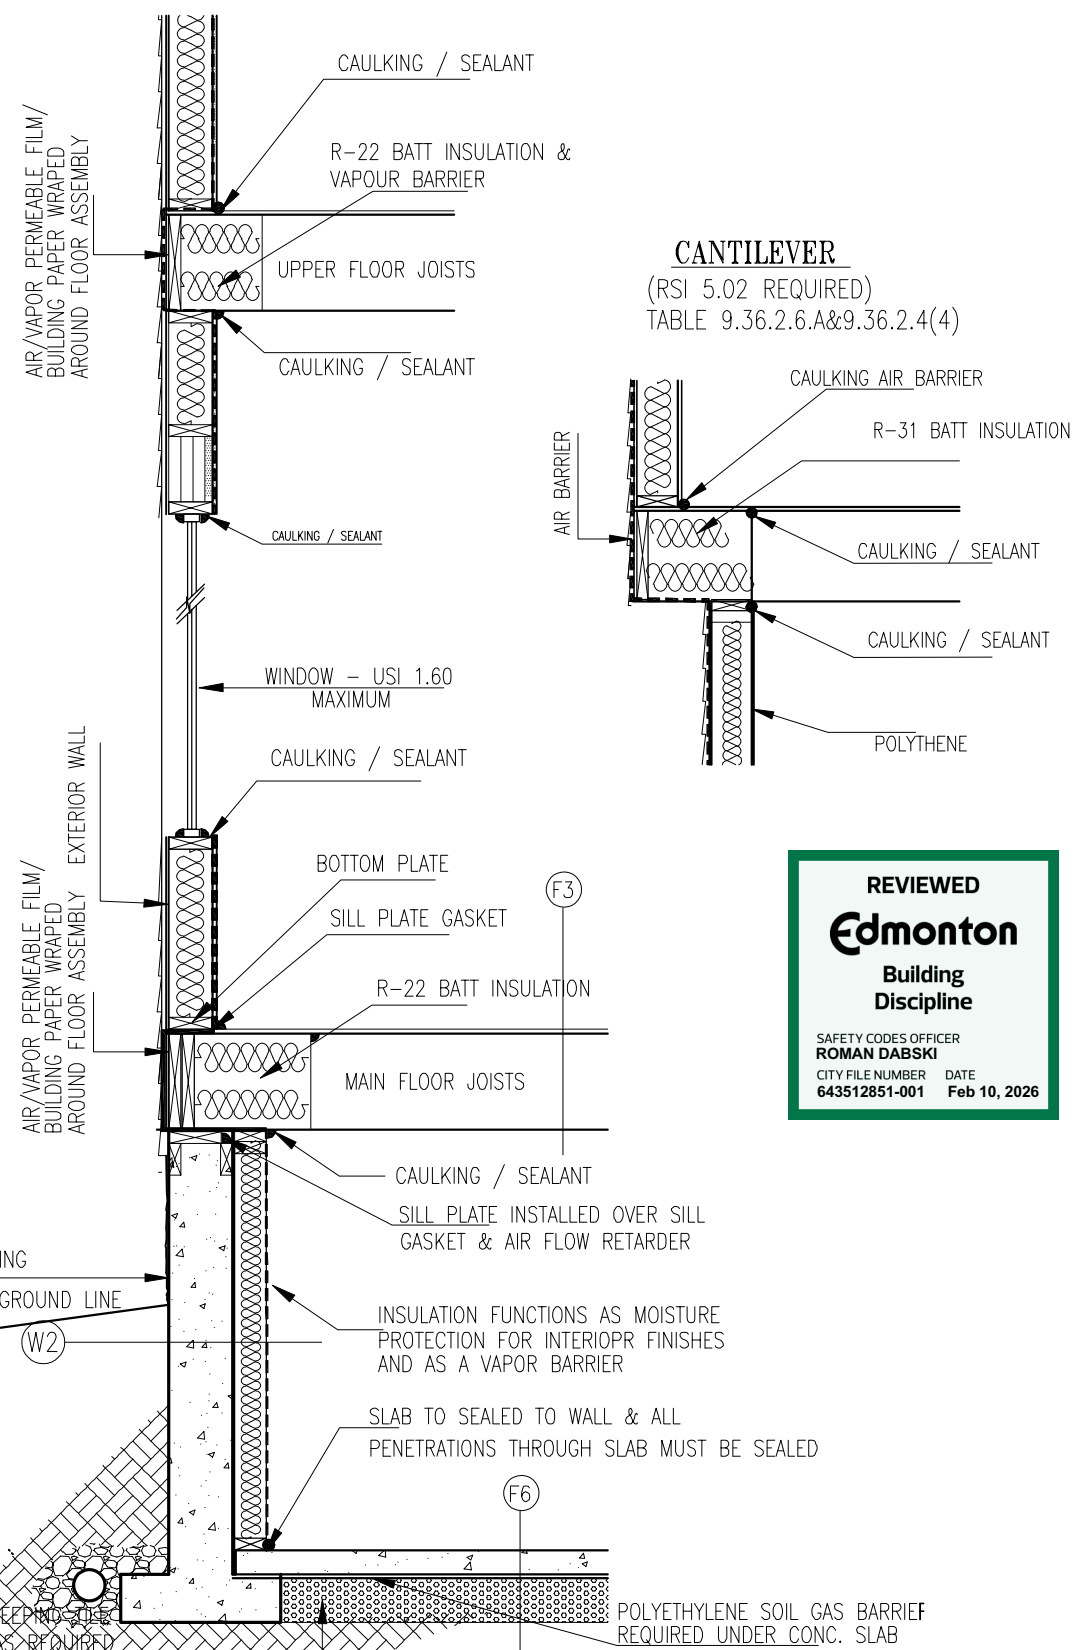


Design Studio-1
for unique designs

16508 - 20 Ave. SW, AB. T6W 5K1
Ph: (780) 951 3628
designstudio-1@hotmail.com


Sant Realty Ab.

AREA:	Scale: As Shown
Main Floor = 1,188 Sqft	Design by: Shahbaz
Upper Floor = 1,416 Sqft	Date: 17 Dec 2025
Total Area = 2,604 Sqft	
Lot : 55	Drawing
Blk.: 4	10 of 11
Plan : 252-0849	
18723 - 131 St NW	
Goodridge Corners	
Edmonton	

PERSCRIPTIVE REQUIREMENTS
THERMAL RESISTANCE FOR ZONE 7A W/HRV

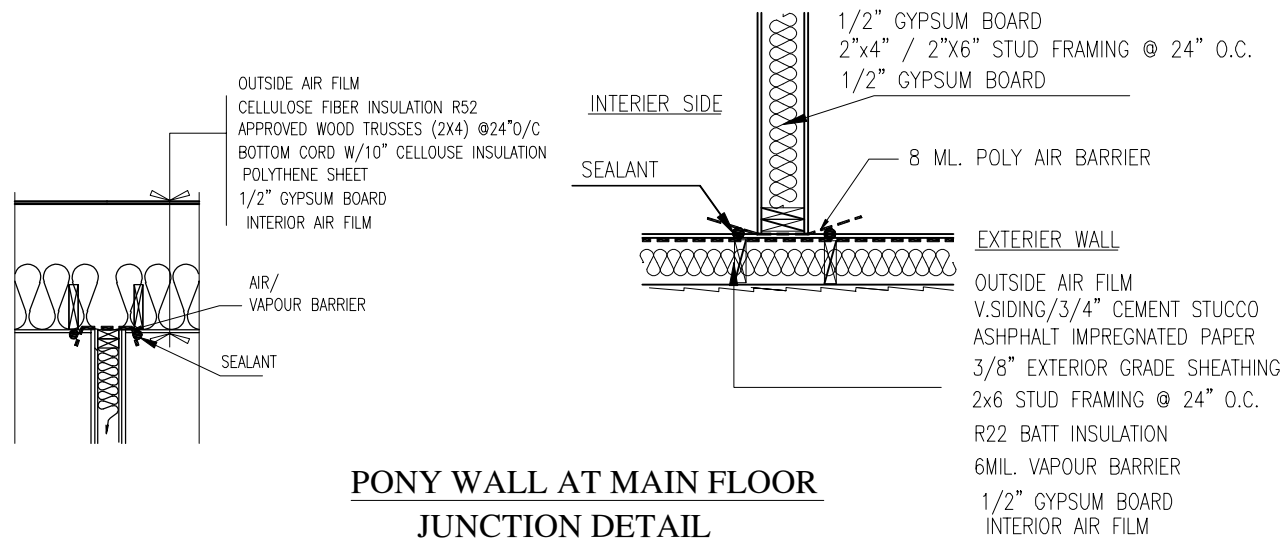


PONY WALL AT MAIN FLOOR
JUNCTION DETAIL

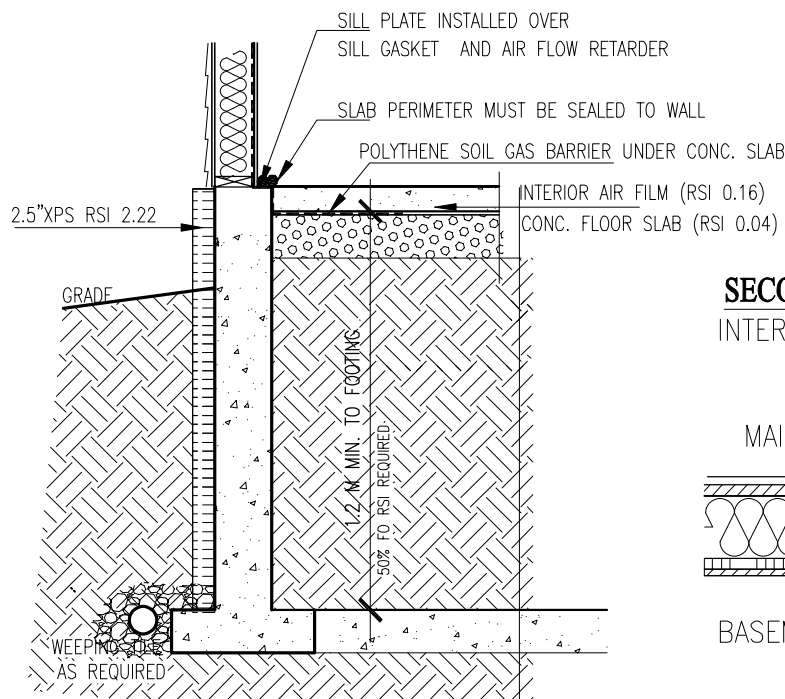



WALKOUT FOUNDATION&UNHEATED FLOOR
(ABOVE FROST LINE-RSI 1.96 W/HRV)
APPENDIX 9.34.2.8.(4)

SECONDARY SUITE SOUND SEPARATION
INTERIOR CEILING/FLOOR ASSEMBLY (STC) 47

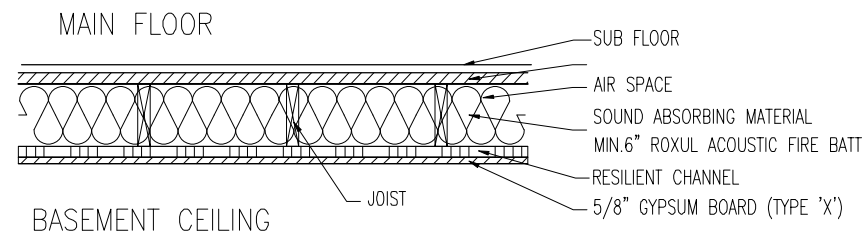

ATTIC ACESS HATCH

RSI 2.60 REQ. (9.36.2.7 (8) & 9.25.3.3(7))

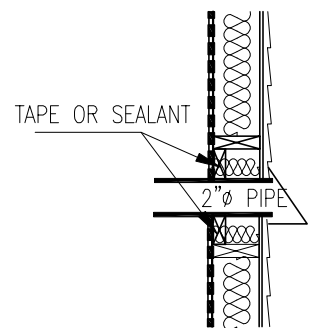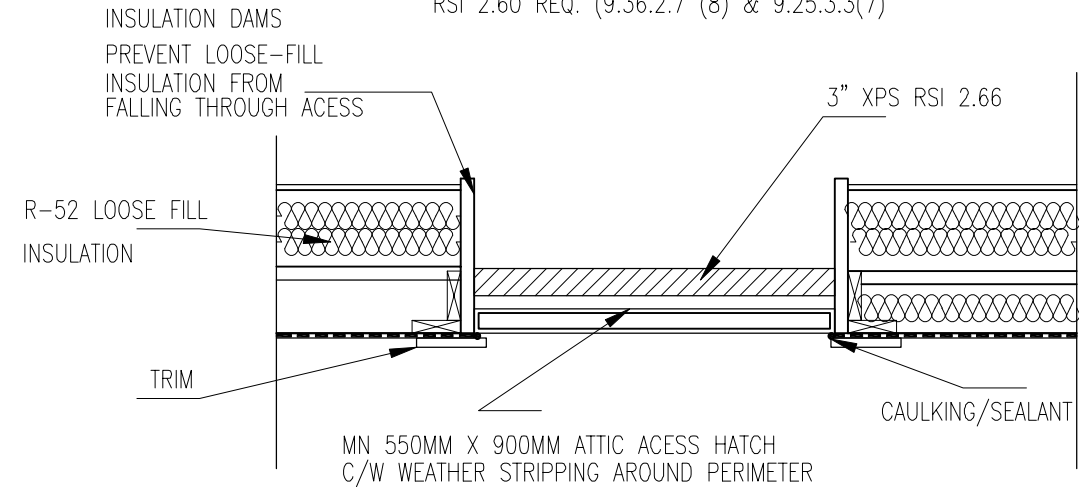

SERVICE PENITRATION
IN EXTERIOR WALL DETAIL

EXTERIOR WALL:
FINISHING MATERIAL AS PER ELEVATION
ASHPALT IMPREGNATED PAPER
3/8" EXTERIOR GRADE SHEATHING
2x6 STUD FRAMING @ 24" O.C.
R22 BATT INSULATION
6MIL. VAPOUR BARRIER
1/2" GYPSUM BOARD

PERFORMANCE REQUIREMENT OF WINDOWS, DOORS & SKYLOGHTS (ABC 9.7.4.3)	
MANUFACTURED AND PRE-ASSEMBLED WINDOWS, DOORS AND SKYLIGHTS AND THEIR INSTALLATION SHALL CONFORM TO: A) AAMA/WDMA/CSA 101/1.5.2/A440, "NAFS-NORTH AMERICAN FEMNESTRATION STANDARD/SPECIFICATION FOR WINDOWS, DOORS AND SKYLIGHTS" (HARMONIZED STANDARD), B) CSA44051,"CANADIAN SUPPLEMENT TO AAMA/WDMA/CSA 101/1.52/A440, NAFS-NORTH AMERICAN FENESTRATION STANDARD/SPECIFICATION FOR WINDOWS, DOORS AND SKYLIGHTS." BUILDING CODE FENESTRATION PERFORMANCE CALCUALTION CALCULATIONS BASED PM AAMA/WDMA/CSA 101/1.5.2/A440-08 (NAFS-08) AND CSA A44051-09	
LOCATION	EDMONTON. AB
TERRAIN TYPE	ROUGH
PERFORMANCE CLASS	R
BUILDING HEIGHT	10 M
MINIMUM PERFORMANCE GRADE (PG)	20
MINIMUM POSITIVE DESIGN PRESSURE	960 PA
MINIMUM NEGATIVE DESIGN PROCEDURE	960 PA
MINIMUM WATER PENETRATION TEST PRESSURE	180 PA
MINIMUM CADNADIAN AIR INFILTRATION/EXFILTRATION	A2

COMPONENT/EQUIPMENT	HEATING/COOLING CAPACITY	STANDARD	MIN PERFORMANCE
GAS-FIRED FORCED AIR FURANCE	< 65.9kW[222,000Btu/h]	CAN/CSA-P.2	>=AFUE 92%
COMPONENT/	INPUT	STANDARD	PERFORMANCE REQ'T
GAS-FIRED HOT WATER TANK	< 22kW[75,000Btu/h]	CAN/CSA-P.3	EF >=0.67-0.0005V
HRV PERFORMANCE			> 60%

Design Studio-1
for unique designs
16508 - 20 Ave. SW,AB. T6W 5K1
Ph: (780) 951 3628
designstudio-1@hotmail.com

Sant Reality Ab.

AREA: Main Floor = 1,188 Sqft Upper Floor = 1,416 Sqft Total Area = 2,604 Sqft	Scale: As Shown Design by: Shahbaz Date: 17 Dec 2025
Lot : 55 Blk.: 4 Plan : 252-0849 18723 - 131 St NW Goodridge Corners Edmonton	Drawing 11 of 11