

16508 - 20 AVE
Customer:

Project No: 18-001

Revision: 1.0

Units: in.

Scale: 1/4" = 1'

Date: 05/14/2026


Sheet Title:

**MAIN
KITCHEN**


Sheet No:

A1

MAIN KITCHEN

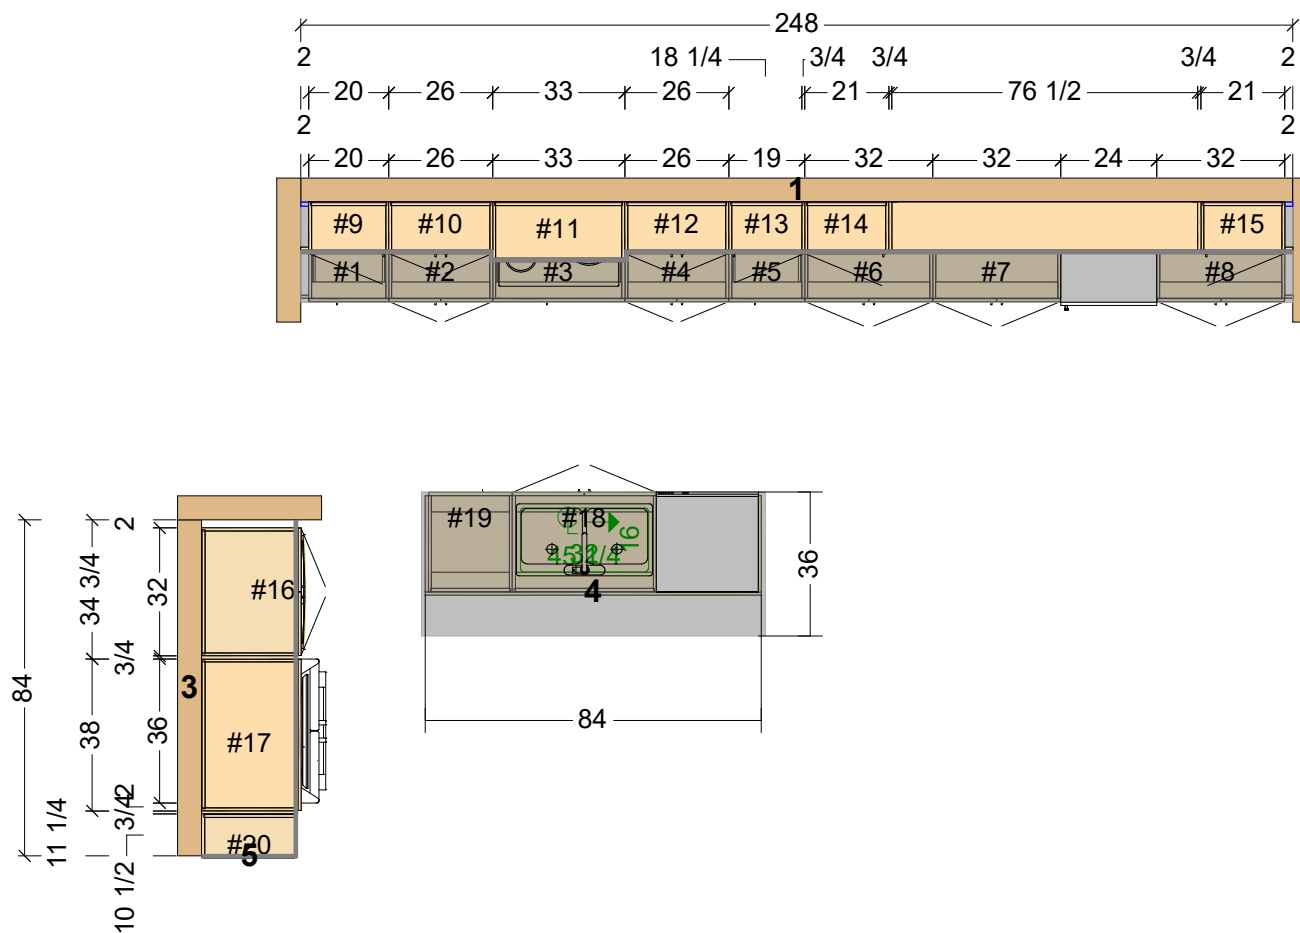

MAIN KITCHEN Wall #1

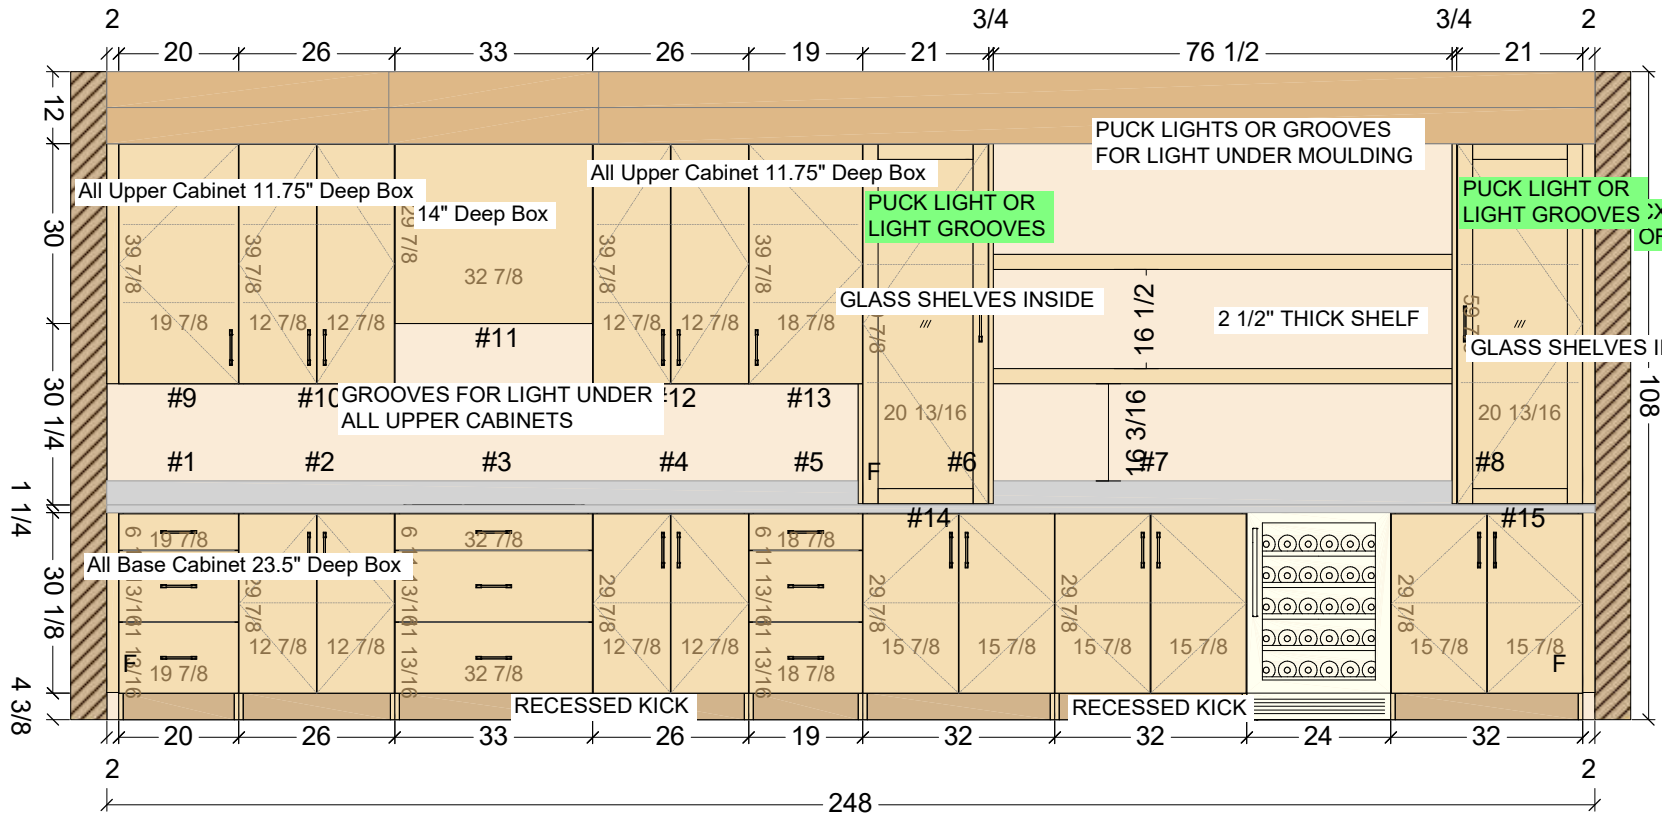

16508 - 20 AV

Customer:


Project No: 18-001
Revision: 1.0
Units: in.
Scale: 3/8" = 1'
Date: 05/14/2026
Sheet Title:

RANGE WALL


Sheet No:

A2


**MAIN
KITCHEN
Wall #5
Back
#20**

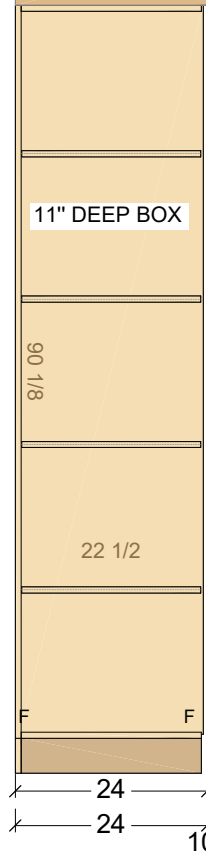

MAIN KITCHEN Wall #3

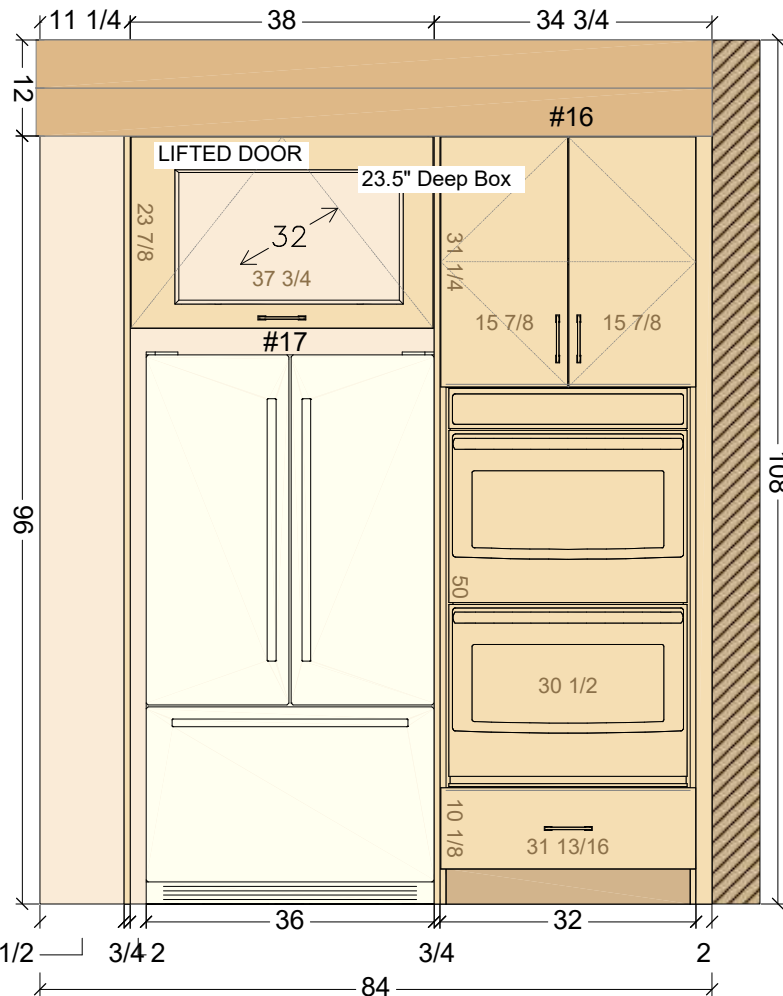

MAIN KITCHEN Wall #4

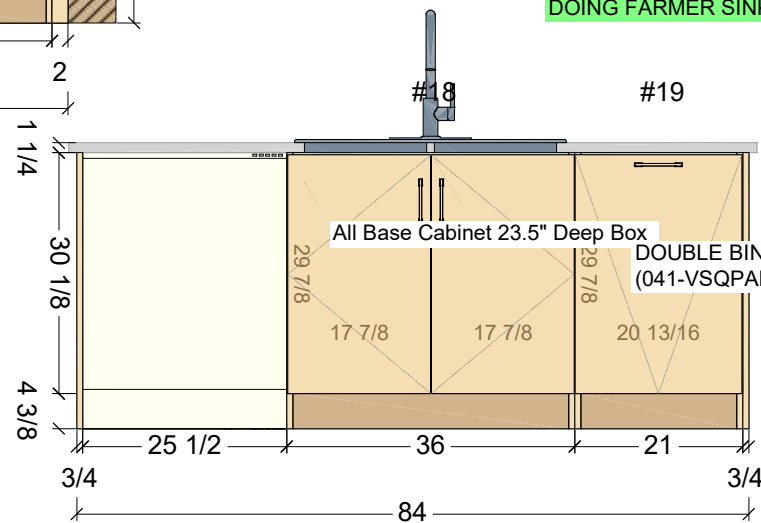

16508 - 20 AVE
Customer:

Project No: 18-001
Revision: 1.0
Units: in.
Scale: 1/2" = 1'
Date: 05/14/2026
Sheet Title:

**FRIDGE
WALL**

Sheet No:

A3

MAIN KITCHEN



16508 - 20 AVE
Customer:

Project No: 18-001

Revision: 1.0

Units: in.

Scale: $\frac{3}{8}'' = 1'$

Date: 05/14/2026

Sheet Title:

**3D MAIN
KITCHEN**

Sheet No:

A4



16508 - 20 AVE
Customer:

Project No: 18-001

Revision: 1.0

Units: in.

Scale: 3/8" = 1'

Date: 05/14/2026


Sheet Title:

**3D ISLAND
MAIN
KITCHEN**


Sheet No:

A5

SPICE KITCHEN

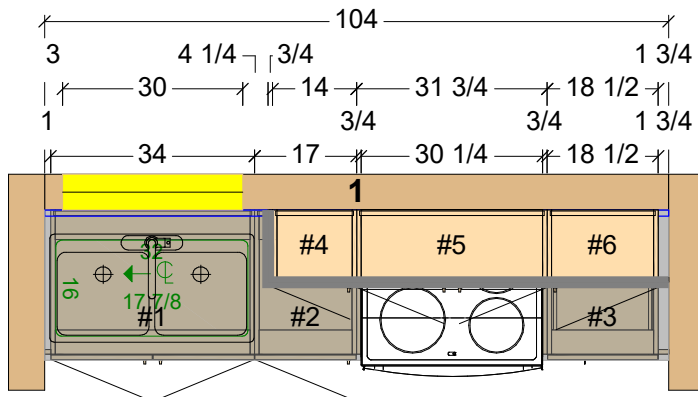

SPICE KITCHEN Wall #1

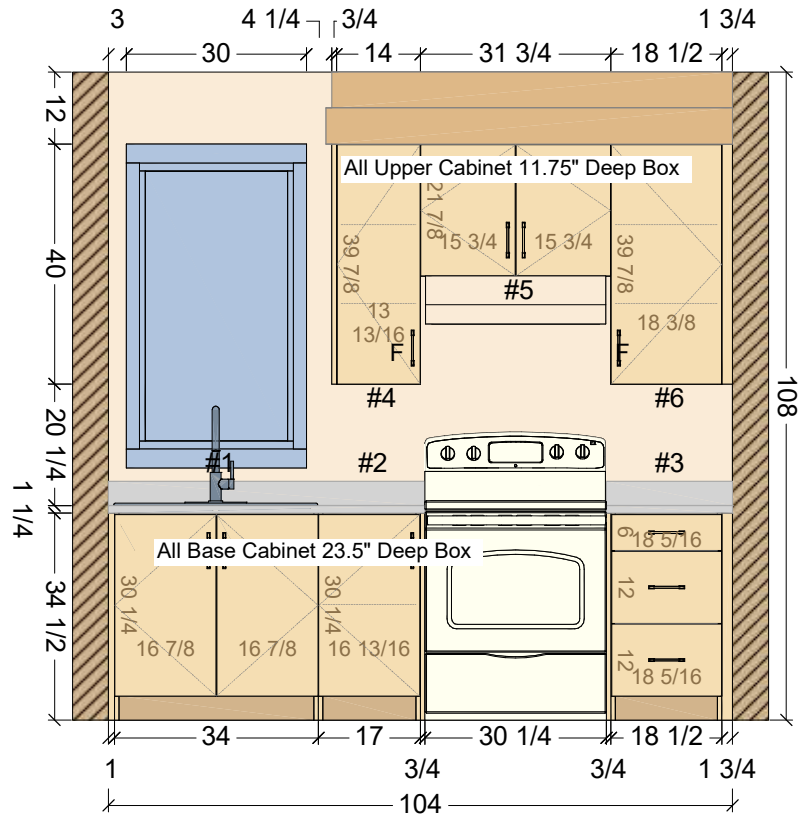

16508 - 20 AVE
Customer:

Project No: 18-001

Revision: 1.0

Units: in.

Scale: 3/8" = 1'

Date: 05/14/2026

Sheet Title:

SPICE KITCHEN

Sheet No:

A6



16508 - 20 AVE
Customer:

Project No: 18-001

Revision: 1.0

Units: in.

Scale: 3/8" = 1'


Date: 05/14/2026

Sheet Title:

**3D SPICE
KITCHEN**

Sheet No:

A7

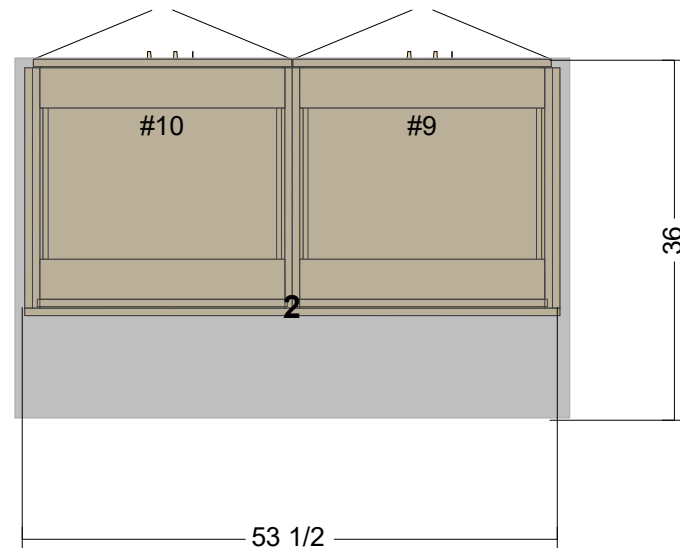[illegible]


Sheet Title:

BASEMENT KITCHEN

Sheet No:

A8

BASEMENT KITCHEN Wall #1

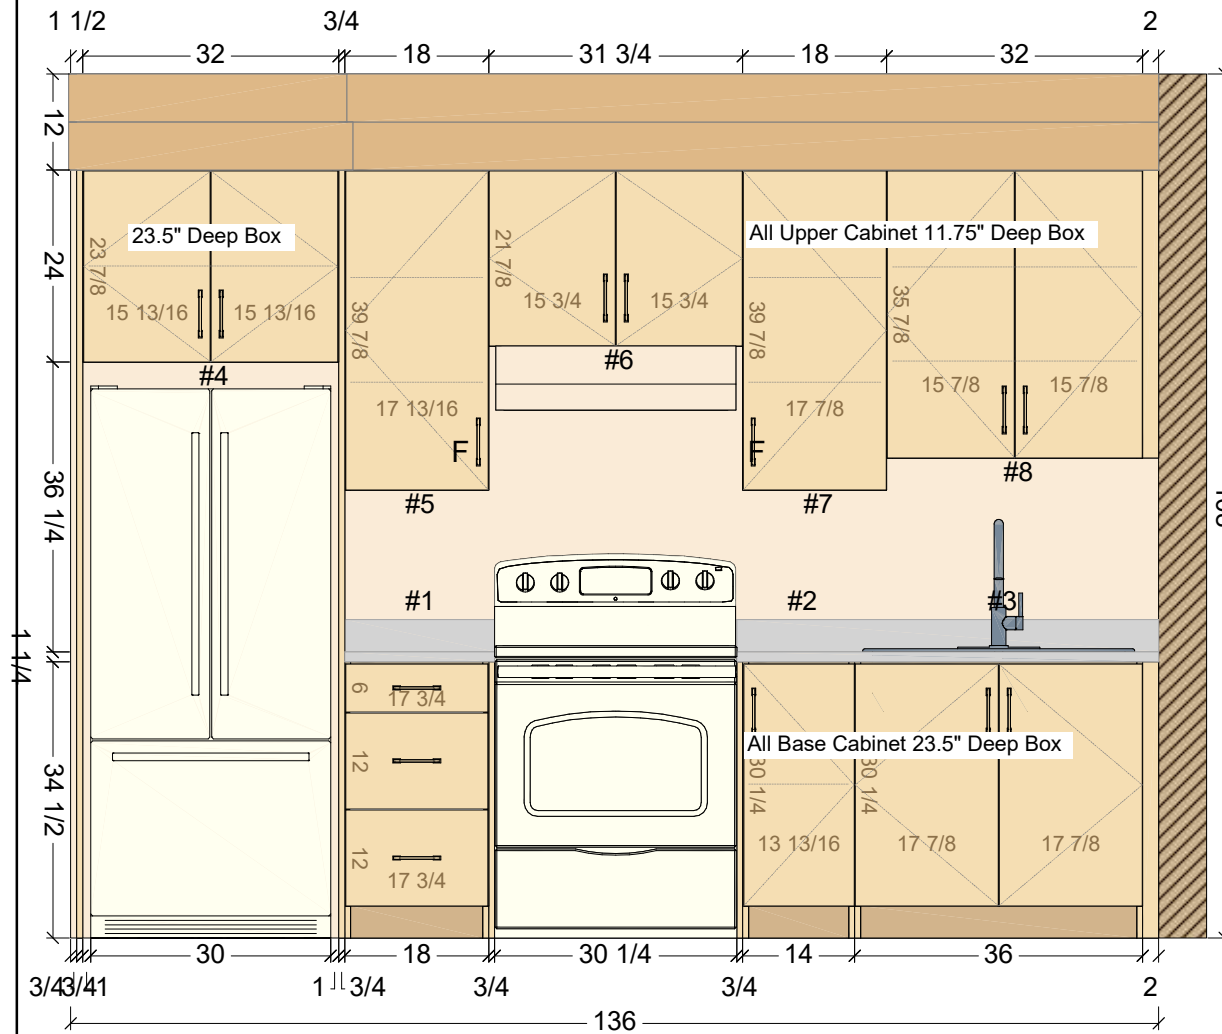

16508 - 20 AVE
Customer:

Project No: 18-001

Revision: 1.0

Units: in.


Scale: 1/2" = 1'

Date: 05/14/2026

Sheet Title:
BASEMENT KITCHEN ELEVATION

Sheet No:

A9

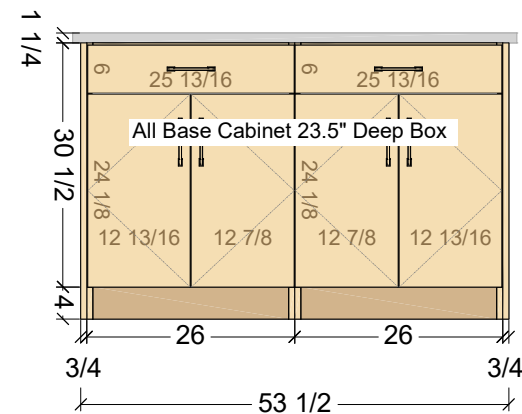



**CANADIAN
WOODMARK**
CABINETS

16508 - 20 AVE
Customer:

Project No: 18-001

Revision: 1.0

Units: in.

Scale: 3/8" = 1'

Date: 05/14/2026

Sheet Title:

**3D
BASEMEN
T KITCHEN**

Sheet No:

A10

Technical drawing showing the layout of a toilet and bidet unit. The toilet is on the left, and the bidet is on the right. Dimensions are provided for the overall width (78), the distance from the wall to the center of the bidet (47 1/4), and the distance from the center of the bidet to the right wall (28). The bidet unit is labeled with a large '1' and a smaller '16' inside a green circle, with a note 'P5 13/16 #1'.

[illegible][illegible]

The diagram illustrates the layout of a bathroom stall. The overall dimensions are 96 inches wide by 63 3/4 inches high. The stall is defined by two vertical walls, each 1 1/4 inches thick. The floor is 69 1/4 inches wide. A toilet is positioned in the center, with a 3/4 inch clearance from the left wall and a 24 inch clearance from the right wall. A vanity unit is located on the right side, with a 2 inch clearance from the right wall. The vanity unit has a width of 23 3/4 inches and a height of 11 7/8 inches. The vanity unit is labeled "RECESSED KICK" and "1".



Sheet Title:

Sheet No: _____

A11

Technical drawing of a three-bay window. The overall width is 84. The bay widths are 32 1/4, 18, and 32 1/4. The overall height is 21. The drawing includes labels for various components: #1 (left bay), #2 (central bay), and #3 (right bay). Dimensions for the bays are 27, 26, and 27. The drawing also shows a central rectangular element labeled #4 and a circular element labeled #5. The drawing is a technical drawing of a three-bay window. The overall width is 84. The bay widths are 32 1/4, 18, and 32 1/4. The overall height is 21. The drawing includes labels for various components: #1 (left bay), #2 (central bay), and #3 (right bay). Dimensions for the bays are 27, 26, and 27. The drawing also shows a central rectangular element labeled #4 and a circular element labeled #5. The drawing is a technical drawing of a three-bay window. The overall width is 84. The bay widths are 32 1/4, 18, and 32 1/4. The overall height is 21. The drawing includes labels for various components: #1 (left bay), #2 (central bay), and #3 (right bay). Dimensions for the bays are 27, 26, and 27. The drawing also shows a central rectangular element labeled #4 and a circular element labeled #5.

[illegible]


Sheet Title:

MASTER BATH


Sheet No:

A12


COMMON BATH

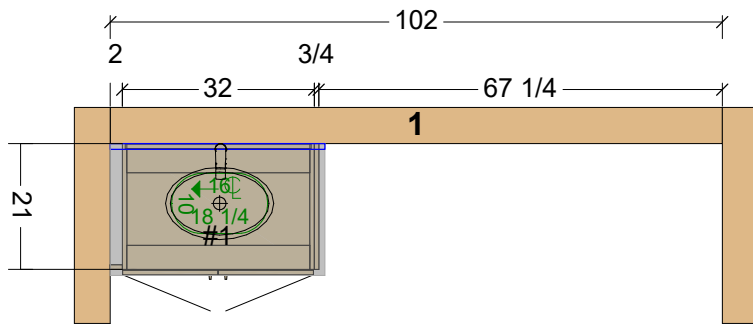


BED 2 BATH

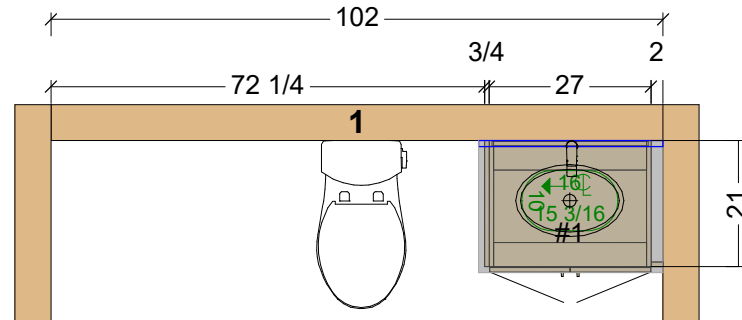

COMMON BATH Wall #1

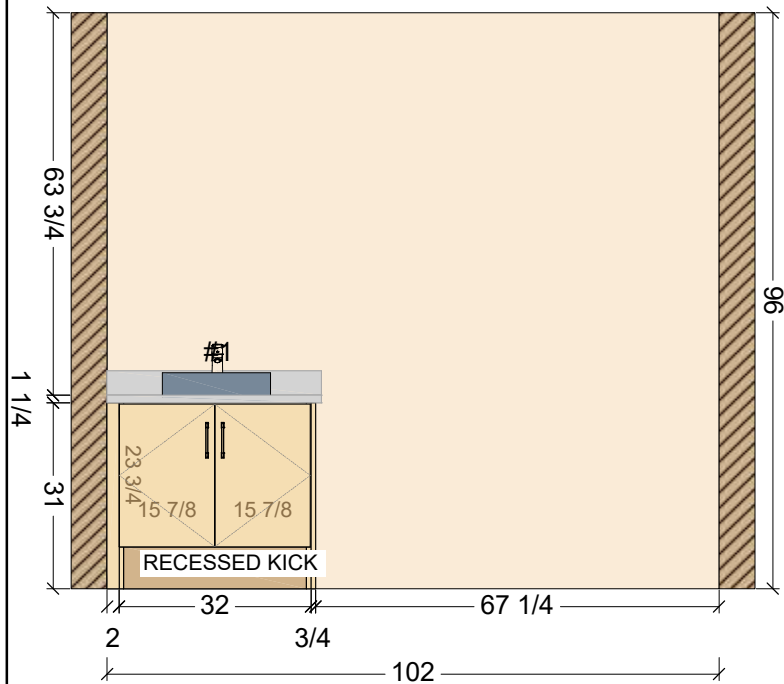

BED 2 BATH Wall #1

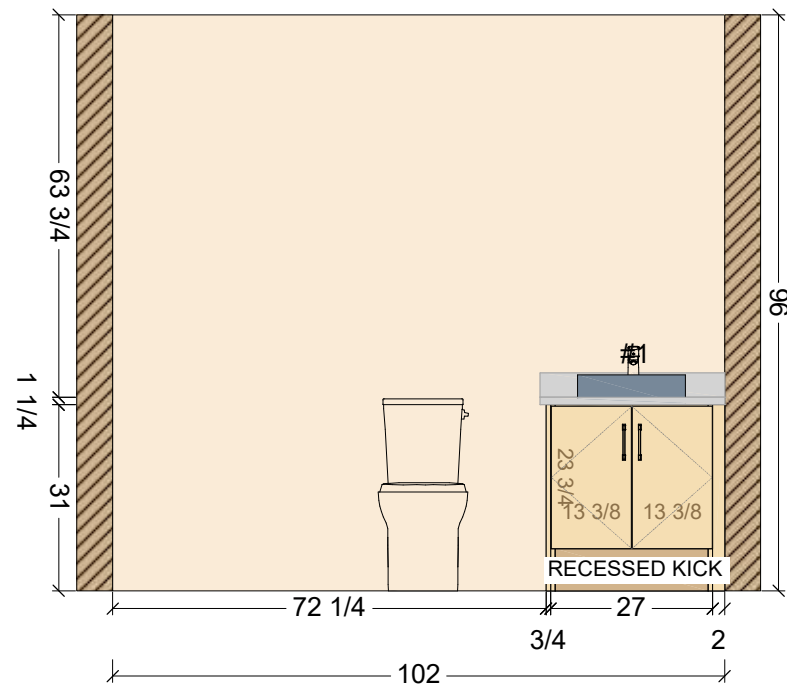

16508 - 20 AVE
Customer:

Project No: 18-001

Revision: 1.0

Units: in.

Scale: 3/8" = 1'

Date: 05/14/2026


Sheet Title:

**COMMON
BATH &
BATH 2**


Sheet No:

A13

BASEMENT BATH

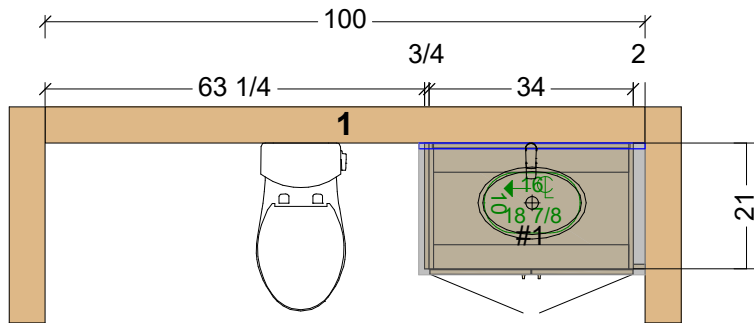

BASEMENT BATH Wall #1

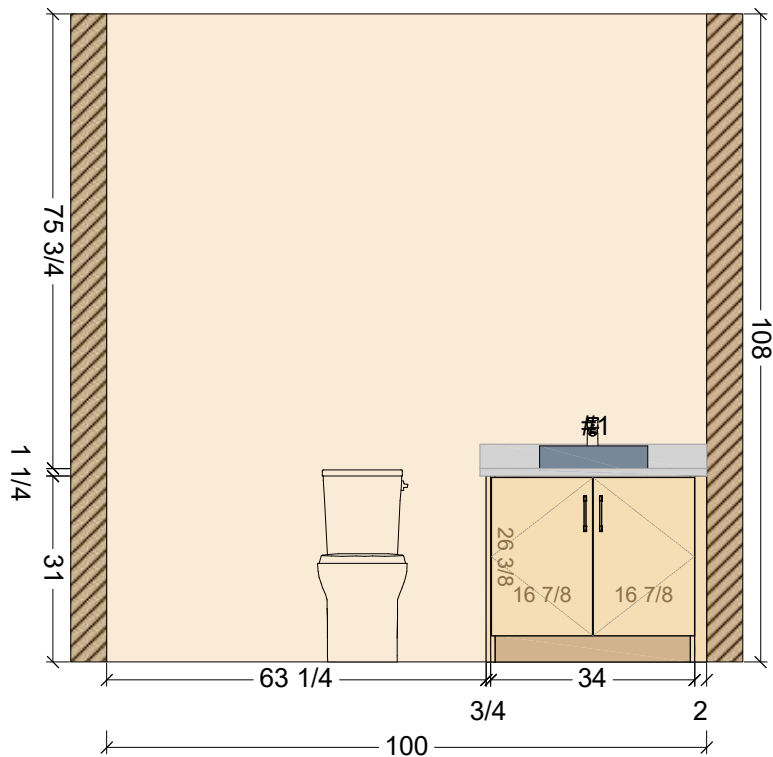

16508 - 20 AVE
Customer:

Project No: 18-001

Revision: 1.0

Units: in.

Scale: 3/8" = 1'

Date: 05/14/2026

Sheet Title:

**BASEMENT
T BATH**

Sheet No:

A14

Technical drawing of a three-door cabinet. The drawing includes a top view and a front elevation. The top view shows a rectangular layout with dimensions: 102 (total width), 32 (left door width), 34 (middle door width), and 32 (right door width). The front elevation shows the cabinet doors with labels #1, #2, and #3. The right door is labeled #1 and has a green outline with dimensions 17 7/8 (width) and 17 7/8 (height). The middle door is labeled #3 and the left door is labeled #2. The cabinet is shown in a light brown color with a dark brown top and bottom. The doors are light brown with a dark brown handle. The drawing is labeled with dimensions and labels #1, #2, and #3.

This detailed floor plan shows the kitchen layout with the following dimensions and features:

- Overall Dimensions:** 102" wide by 108" deep.
- Upper Cabinets:** Labeled "All Upper Cabinet 11.75" Deep Box". They are 36" high and 32" deep. The layout includes three sets of doors with widths of 15 7/8", 16 7/8", and 15 7/8" respectively. The total width of the upper cabinet section is 96" (32" + 34" + 32").
- Base Cabinets:** Labeled "All Base Cabinet 23.5" Deep Box". They are 24 1/4" high. The layout includes two 27" wide doors for the refrigerator and a 34" wide door for the sink. The total width of the base cabinet section is 96" (27" + 27" + 6" + 34").
- Appliances:** A refrigerator is shown on the left, and a sink with a faucet is shown on the right.
- Dimensions:** The total width is 102" (3" + 27" + 27" + 6" + 34" + 2"). The total depth is 108" (12" + 36" + 24 1/4" + 34 1/2" + 1 1/4").
- Other Labels:** "RECESSED KICK" is indicated at the bottom right of the base cabinet section.



**CANADIAN
WOODMARK**
CABINETS

16508 - 20 AVE

Customer:

Project No: 18-001

Revision: 1.0

Units: in.

Scale: $3/8" = 1'$

Date: 05/14/2026

Sheet Title:

LAUNDRY

Sheet No:

A15

MAIN FLOOR BATH



DEN BATH



16508 - 20 AVE
Customer:

Project No: 18-001

Revision: 1.0

Units: in.

Scale: 3/8" = 1'

Date: 05/14/2026

Sheet Title:

3D

Sheet No:

A16

MASTER BATH



BED 2 BATH



COMMON BATH



CANADIAN
WOODMARK
CABINETS

16508 - 20 AVE
Customer:

Project No: 18-001

Revision: 1.0

Units: in.

Scale: 3/8" = 1'

Date: 05/14/2026

Sheet Title:

3D

Sheet No:

A17



16508 - 20 AVE
Customer:

Project No: 18-001

Revision: 1.0

Units: in.

Scale: 3/8" = 1'

Date: 05/14/2026

Sheet Title:

3D
LAUNDRY

Sheet No:

A18